

BRANDSCHUTZPLAN



SML Maschinen GmbH

Gewerbepark Ost 32

4846 Redlham

Plannummer	Bezeichnung	Hauptsächliche Nutzung	Plandatum
A		Planzeichenlegende	7.09.2024
B		Brandalarmplan	7.09.2024
C		Meldergruppenverzeichnis	13.08.2024
0	Lagebild		7.09.2024
0.1	Plannummern		7.09.2024
0.2	Sprinklerübersicht		7.09.2024
0.3	Dachfläche		7.09.2024
1	Lageplan		7.09.2024
2	Untergeschoss	Umkleiden, Lüftungszentrale KG	7.09.2024
3	Untergeschoss	Wärmegewinnung, EDV-Server, Aufenthalt, Umkleide KG	7.09.2024
4	Untergeschoss	Mediengänge Halle 9/10, Sprinklerzentrale, Druckluft,	
		Strahlerraum, NSHV KG	7.09.2024
5	Untergeschoss	Mediengänge Halle 5/6/9, KG	7.09.2024
6	Untergeschoss	Mediengänge 5/6, KG	7.09.2024
7	Erdgeschoss	Empfang/Foyer, Kantine-Küche, Besprechung EG,	
		(Hauptgebäude, Verbindungstrakt)	7.09.2024
8	Erdgeschoss	Lackiererei, Lager Kalt (Halle 2)	7.09.2024
9	Erdgeschoss	Warmlager, QS, Lackiererei, Lager kalt, (Halle 1,2)	7.09.2024
10	Erdgeschoss	WE Süd, Warmlager, QS, (Halle 1)	7.09.2024
11	Erdgeschoss	Warmlager, E-Werkstatt+Rohrleger, Baugruppenfertigung,	
		(Halle 1, 3, 4)	7.09.2024
Verteiler: 2x Feuerwehr ; 1x bei BMZ ; 1x BSB			

Feld für Vidierung:

Planverfasser: TB JOSEF LEITNER



Hörzinghaider Strasse 3

A - 4623 Gunskirchen

Tel.: 07246/8617- 10

0664/3031130

office@tb-leitner.co.at

BRANDSCHUTZPLAN



SML Maschinen GmbH

Gewerbepark Ost 32
4846 Redlham

Plannummer	Bezeichnung	Hauptsächliche Nutzung	Plandatum
12	Erdgeschoss	E-Werkstatt+Rohrleger, Baugruppenfertigung,	
		Baugruppenfertigung hybrid (Halle 3, 4, 5)	7.09.2024
13	Erdgeschoss	Instandhaltungswerkstatt, Werkzeugausgabe, Pyrolyse,	
		Musterlager, Technikum (Halle 9, 10)	7.09.2024
14	Erdgeschoss	Granulatlager, Abfall-Abholung, Technikum (Halle 9, 10)	7.09.2024
15	Erdgeschoss	Linienfertigung, Versand, Zwischenlager (Halle 6, 7, 8)	7.09.2024
16	Erdgeschoss	Baugruppenfertigung hybrid, Linienfertigung (Halle 5, 6)	7.09.2024
17	Erdgeschoss	Versand, Zwischenlager (Halle 7, 8)	7.09.2024
18	Erdgeschoss	Versand, Zwischenlager kalt, Abfall-Abholung (Halle 7,8,9)	7.09.2024
19	Erdgeschoss	Lagerhalle 11 und 12	7.09.2024
20	1.Obergeschoss	Veranstaltung, Büro 1.OG, (Hauptgebäude,	
		Verbindungstrakt)	7.09.2024
21	1.Obergeschoss	Büro 1.OG (Verbindungstrakt)	7.09.2024
22	1.Obergeschoss	Büro 1.OG (Halle 3)	7.09.2024
23	2.Obergeschoss	Büro 2.OG (Hauptgebäude)	7.09.2024
24	2.Obergeschoss	Stiegenhaus 2.OG (Stiege 3-Verbindungstrakt)	7.09.2024
25	3.Obergeschoss	Büro 3.OG (Hauptgebäude)	7.09.2024

Verteiler: 2x Feuerwehr ; 1x bei BMZ ; 1x BSB

Planverfasser: TB JOSEF LEITNER



Hörzinghaider Strasse 3







A - 4623 Günskirchen

Tel.: 07246/8617- 10



0664/3031130

office@tb-leitner.co.at

PLANZEICHENLEGENDE

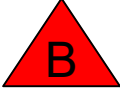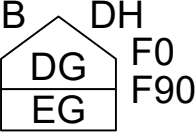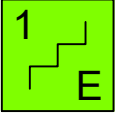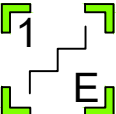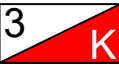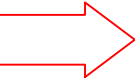	Brandabschnittsgrenze		Nicht mit Wasser löschen
	Rauchschräge		Erhöhte Brandgefahr
	Brandschutztür		Explosionsgefahr
	Brandbrücke		Gefahr durch Chemikalien
	Kennzeichnung der Brandwiderstandsklasse der Decken und Bedachung		Gefahr durch Elektrizität
	Notausgang		Gefahr durch radioaktive Stoffe
	Stiegenhaus (brandschutztechnisch abgeschlossen)		Rauchmelder
	offene Verbindungsstiege ohne brandschutztechnischen Abschluss		Temperaturmelder
	Notleiter/Aufstiegsleiter		Rauchmelder in Zwischenboden
	Schacht		Rauchmelder in Zwischendecke
	Aufzug		Druckknopfmelder
	Hauptabspernung Wasser		Lüftungsleitungsmelder
	Hauptabspernung Gas		Alle Brandfallsteuerungen EIN
	Hauptabspernung Heizung		Auslösestelle Hausalarm
	Elektroverteiler-Hauptschalter		Auslösestelle der Stiegenhausentrauchung
	Elektroverteiler		
	Feuerwehrhauptzugang		
	Feuerwehrgang		

PLANZEICHENLEGENDE

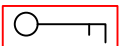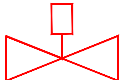1/0			
	Linearmelder		Trockensteigleitung Einspeisestelle
	Blitzleuchte		Trockensteigleitung Schlauchanschluss
	Brandmelderzentrale Hauptmelder		Löschwasserbehälter
	Brandmelderzentrale		
	Brandmelder-Parallelanzeige		Saugstelle
	Feuerwehrbedienfeld		
	Abgesetztes Bedienfeld		Wasserlöschanlage
	Feuerwehr Plankasten		Gaslöschanlage Pulverlöschanlage Sauerstoffreduktionsanlage
	Auslösestelle Rauchwärmeabzug		Sprinklerzentrale
	Schlüsselsafe		Löschmittelzentrale
	Schlüsselbox für sonstigen Zugang		Sauerstoff - Reduzieranlage - Steuerzentrale
	Rauchwärmeabzug		0001 Strömungswächter
	Rauchabzug		Erste-Hilfe Einrichtung
	Sirene		Spannungsfreischalter für Photovoltaikanlage
	Handfeuerlöscher		Übergabeschränk: (Wechselrichter, Trafo, Phasensync.,)
	Defibrillator		
	Unterflurhydrant		Lage der PV-Module
			Defibrillator
	Wandhydrant Entnahmestellen mit A-Kupplung		
	Wandhydrant 2b: nasse Löschwasseranlage mit Wandhydranten mit C-Festkupplung, geeignet zur gleichzeitigen Verwendung von zwei Entnahmestellen		
	Sammelplatz		

Brandalarmplan

SML Maschinen GmbH
Gewerbepark Ost 32
4846 Redlham

Feuerwehr: **NOTRUF 122**

Rotes Kreuz : **NOTRUF 144**

Polizei: **NOTRUF 133**

Gebäudemanagement: **Hr. Ing. Thomas Grafinger**
Tel.: 0676 / 889 122 95


Brandschutzbeauftragter.: **Hr. Daniel Ennser**
Tel.: 0676 / 889 124 66

BSB-Stv.: **Hr. Klaus Pötsch**
Tel.: 0676 / 889 124 15

Hr. Patrick Weingartner
Tel.: 0676 / 889 124 78

Hr. Julian Neudorfer
Tel.: 0660 / 758 50 11

50 Meter Raster

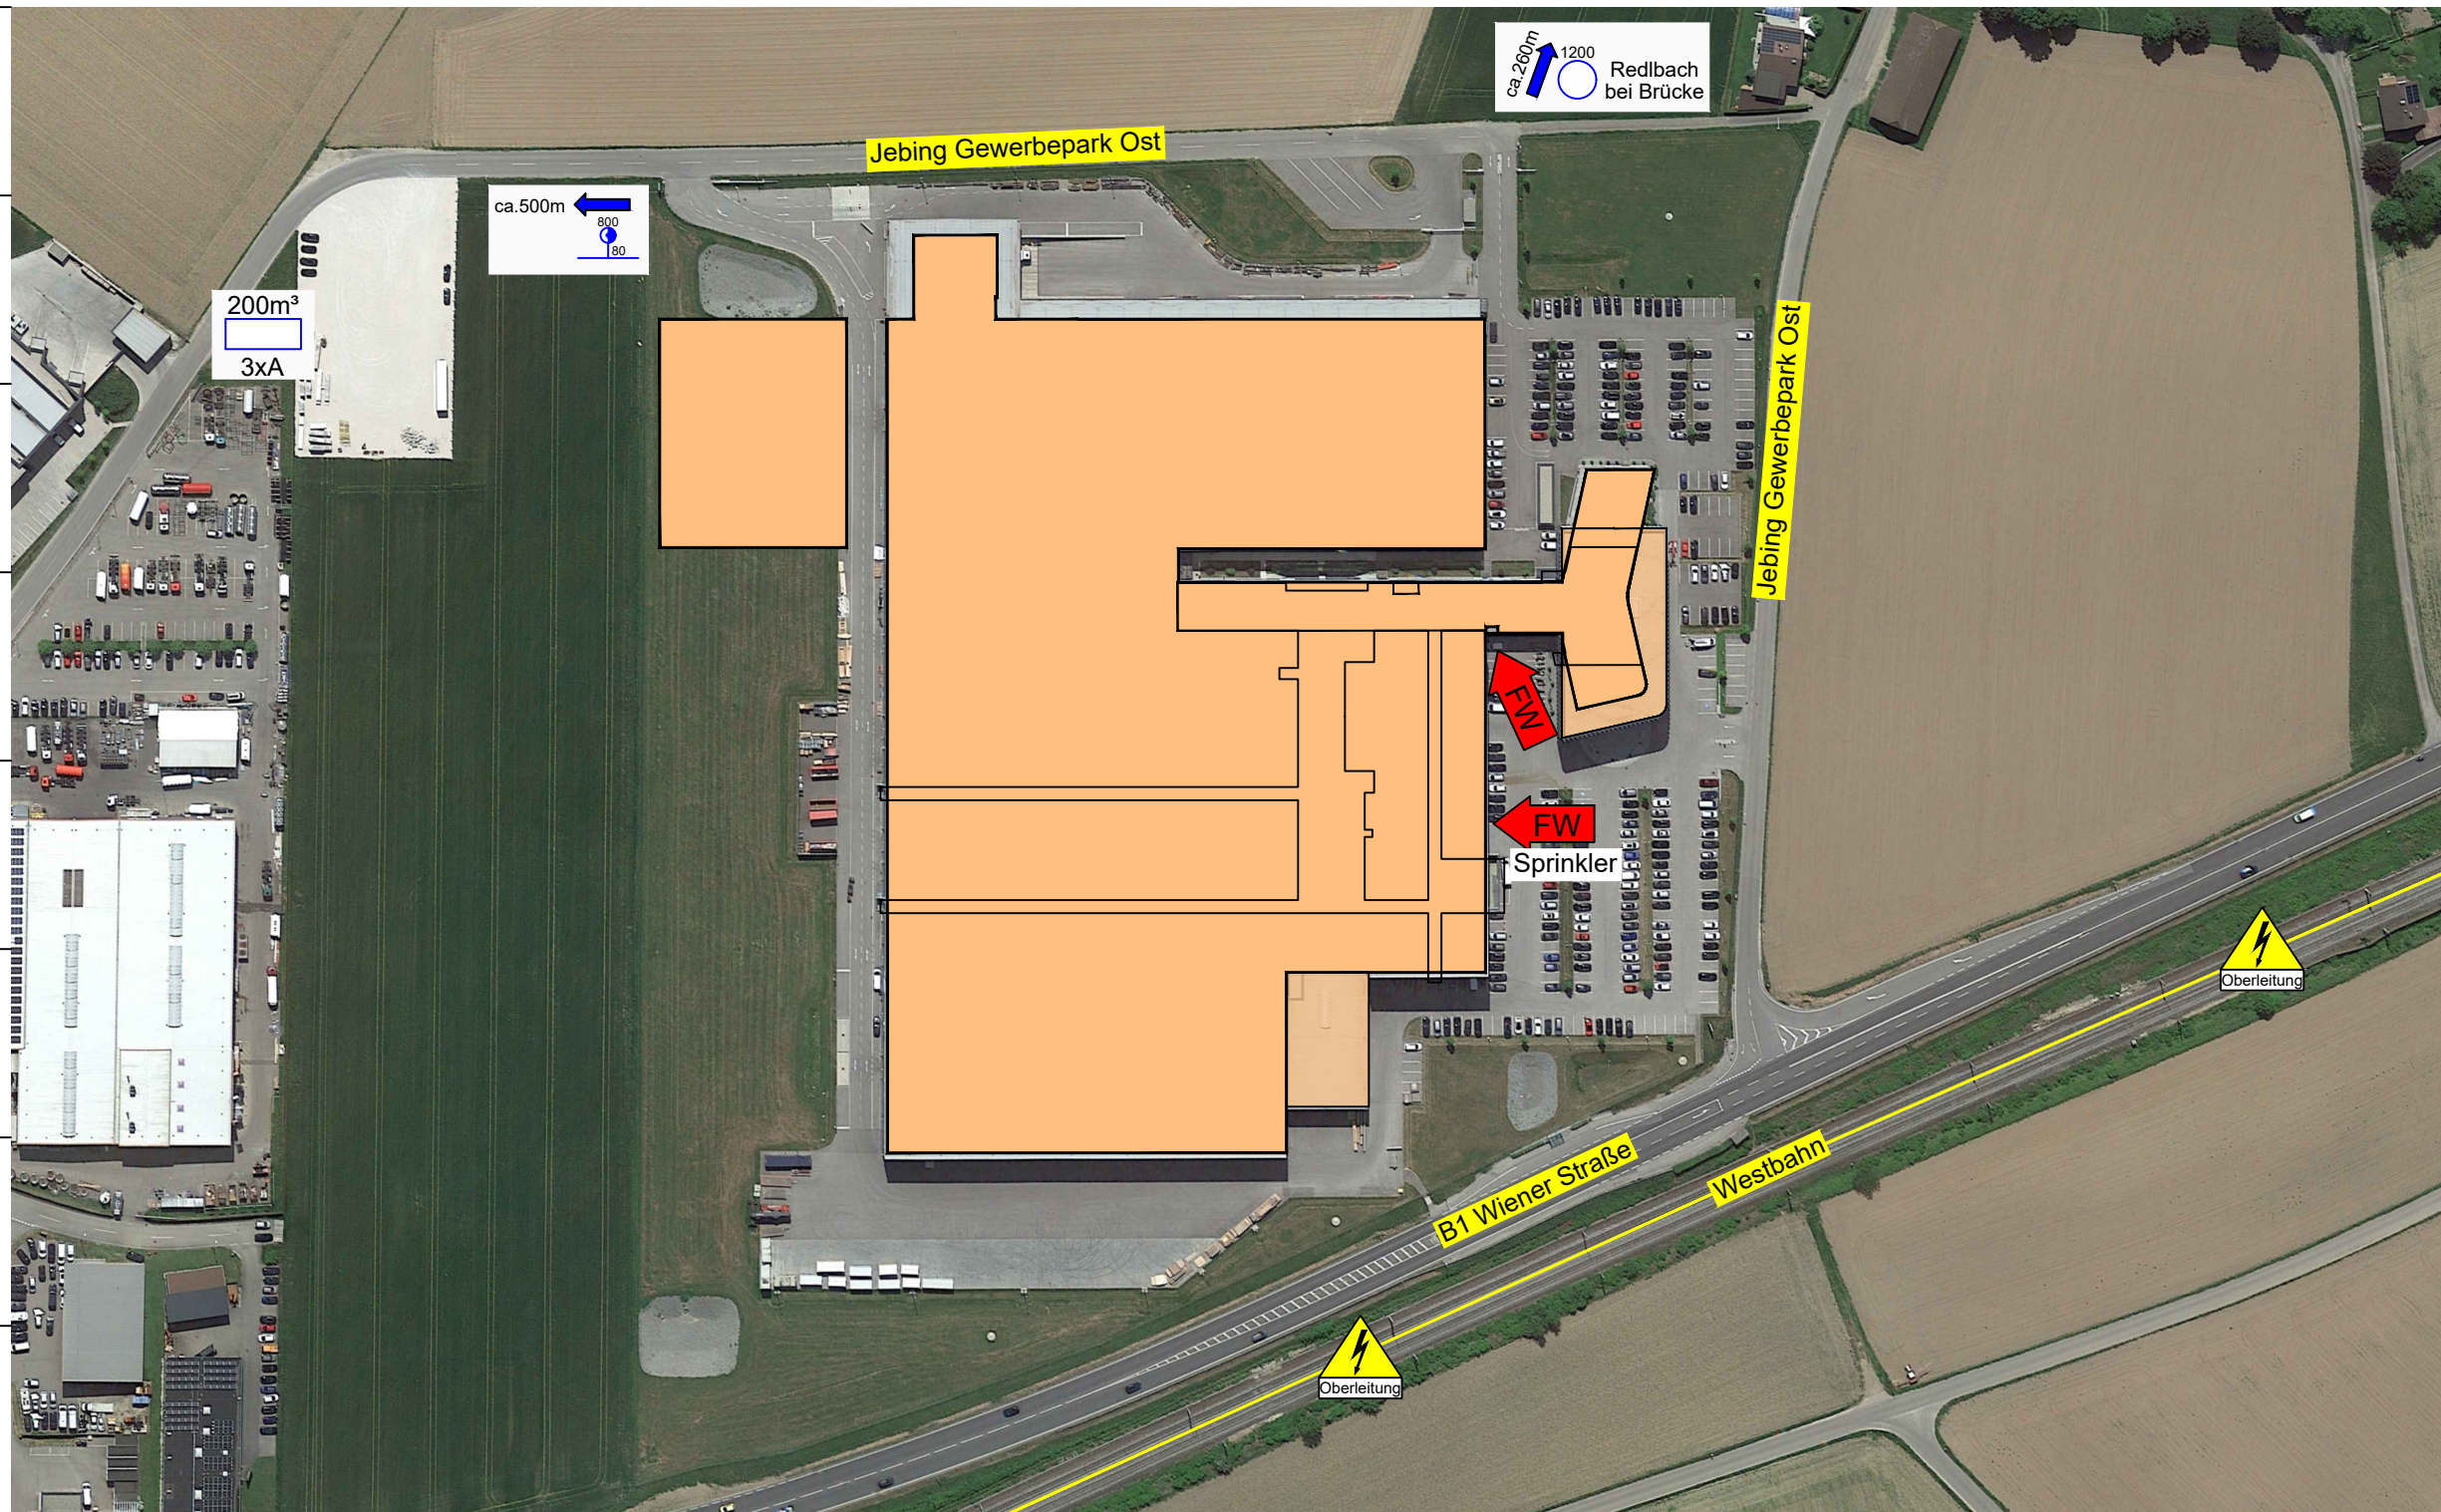

50 Meter Raster



Unterflurhydrant




Gefahr durch Elektrizität



Löschwasserbehälter



Saugstelle

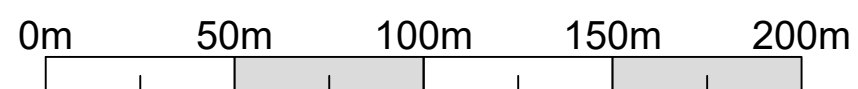

BRANDSCHUTZPLAN

SML Maschinengesellschaft mbH

Gewerbepark Ost 32, 4846 Redlham

Lagebild

Maßstab 1:2000

Stand: 7.09.2024


Plan Nr. **00** von **25**




TB JOSEF LEITNER
Hörzinghaider Strasse 3
A - 4623 Gunskirchen




Kellergeschoss

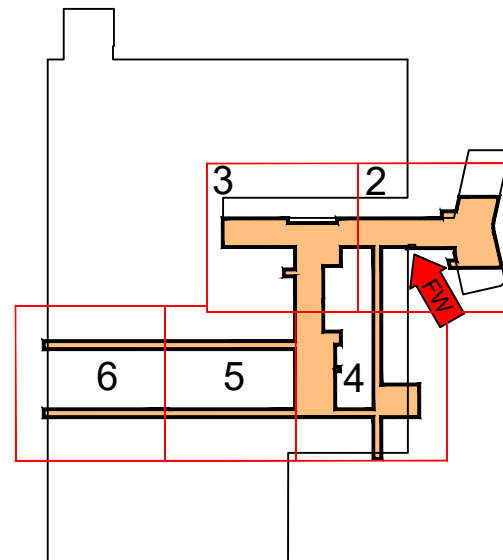


Erdgeschoss

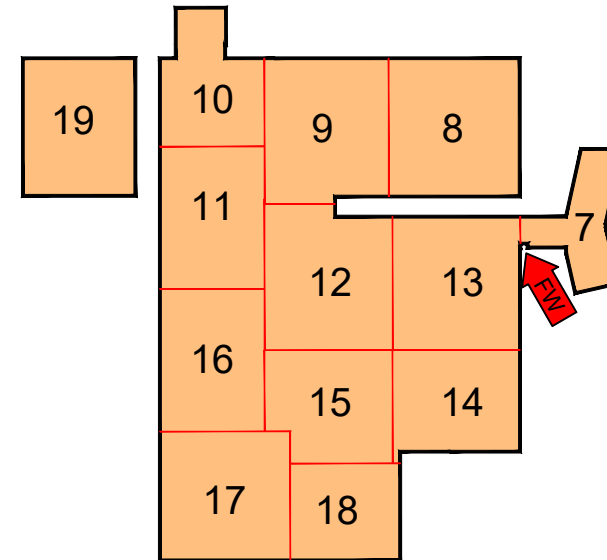


1.Obergeschoss

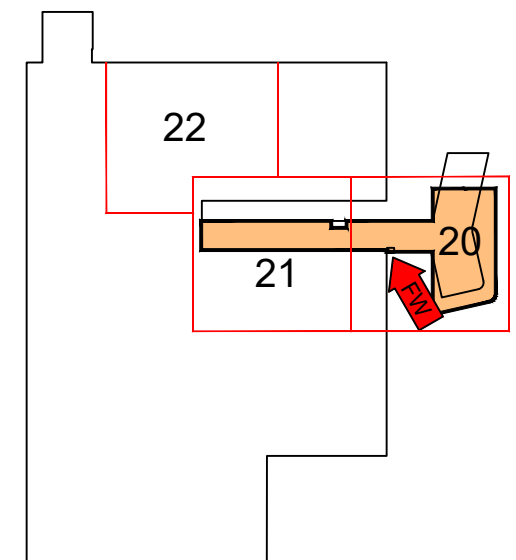

2.Obergeschoss

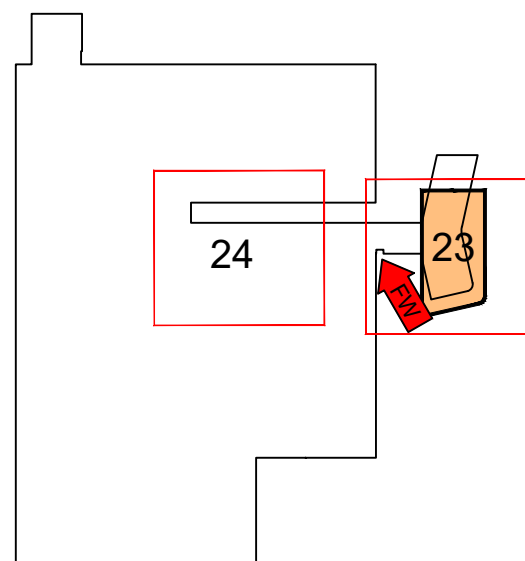

3.Obergeschoss

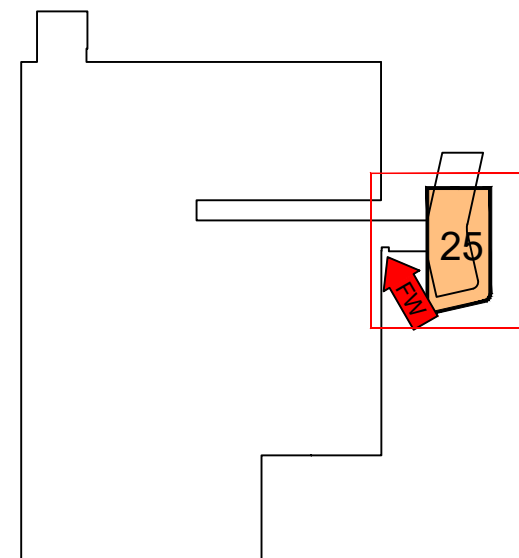

BRANDSCHUTZPLAN

SML Maschinengesellschaft mbH


Gewerbepark Ost 32, 4846 Redlham

Übersicht Plannummern

Maßstab 1:2000

Stand: 7.09.2024


Plan Nr. **0.1** von **25**

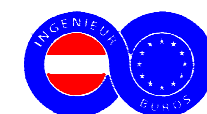


TB JOSEF LEITNER
Hörzinghaider Strasse 3
A - 4623 Gunskirchen




Kellergeschoss

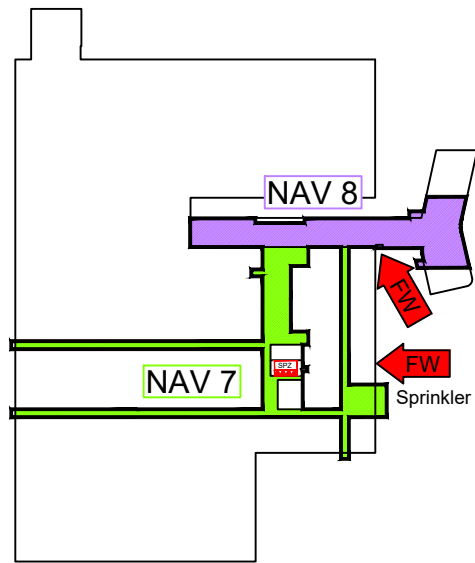


Erdgeschoss

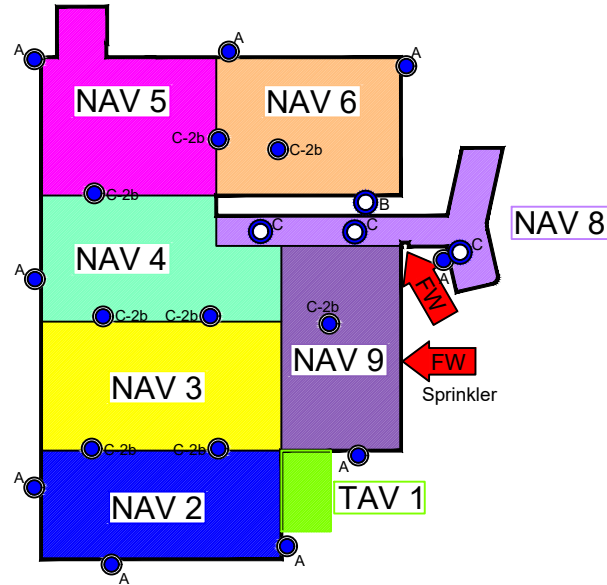


1.Obergeschoss

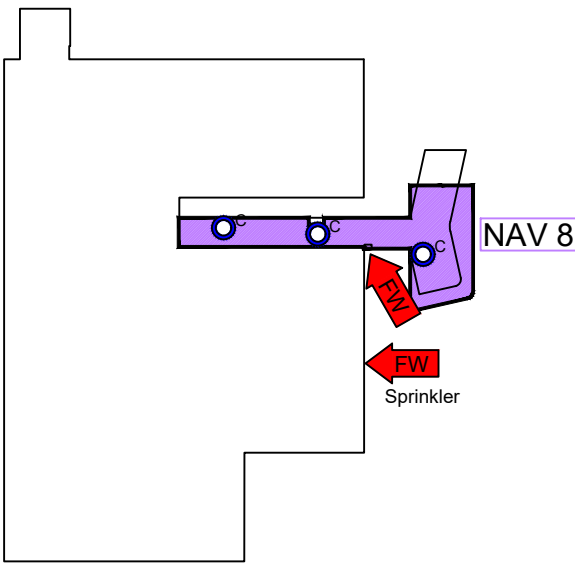


2.Obergeschoss

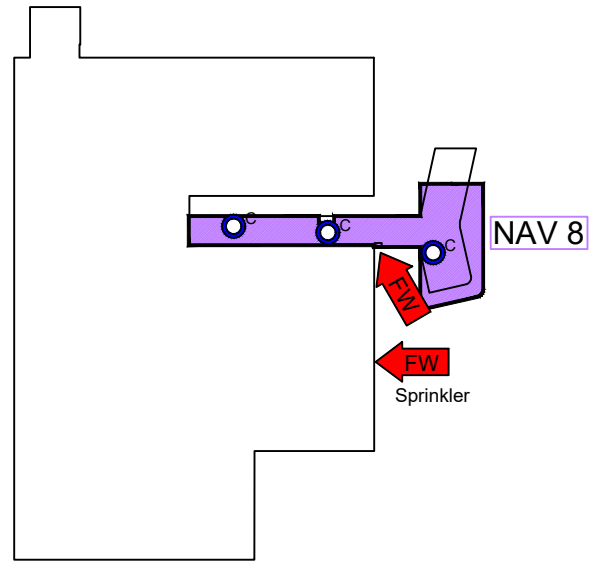

3.Obergeschoss

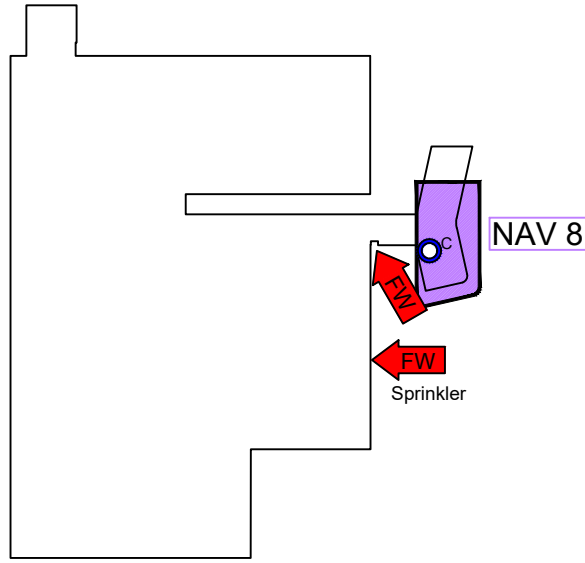

BRANDSCHUTZPLAN		
SML Maschinengesellschaft mbH		
Gewerbepark Ost 32, 4846 Redlham		
Übersicht Sprinkler		
Maßstab	Stand: 7.09.2024	Plan Nr. 0.2 von 25
		TB JOSEF LEITNER Hörzinghaider Strasse 3 A - 4623 Gunskirchen

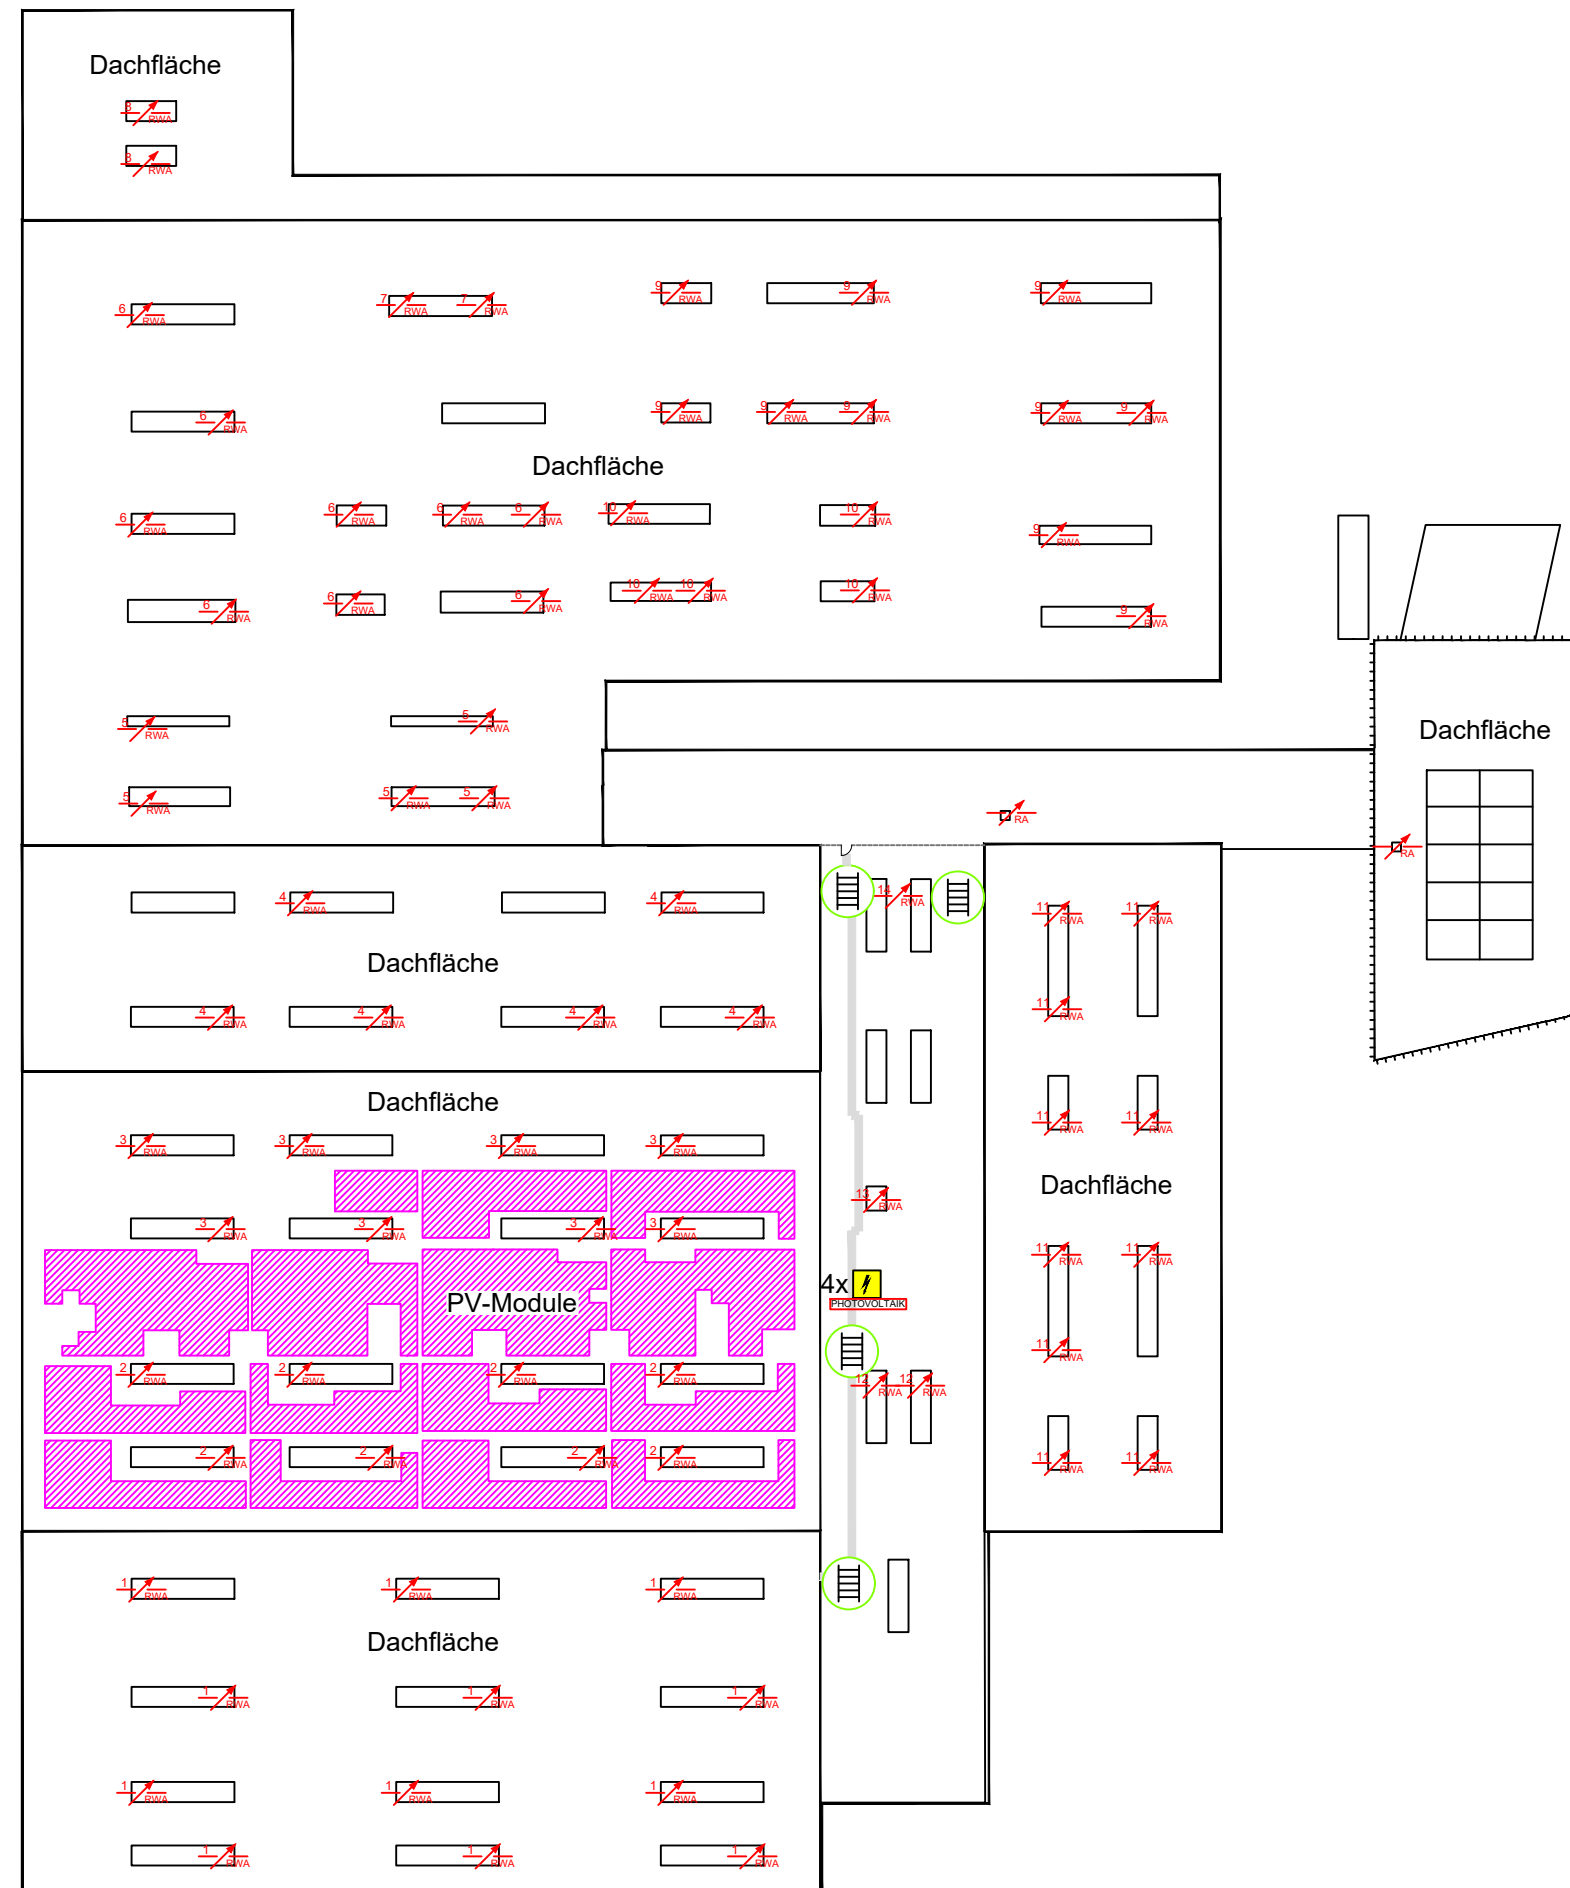

BRANDSCHUTZPLAN


SML Maschinengesellschaft mbH
Gewerbepark Ost 32, 4846 Redlham

Übersicht Dachfläche

Maßstab Stand: 7.09.2024 Plan Nr. **0.3** von **25**



TB JOSEF LEITNER
Hörzinghaider Strasse 3
A - 4623 Gunsirichen

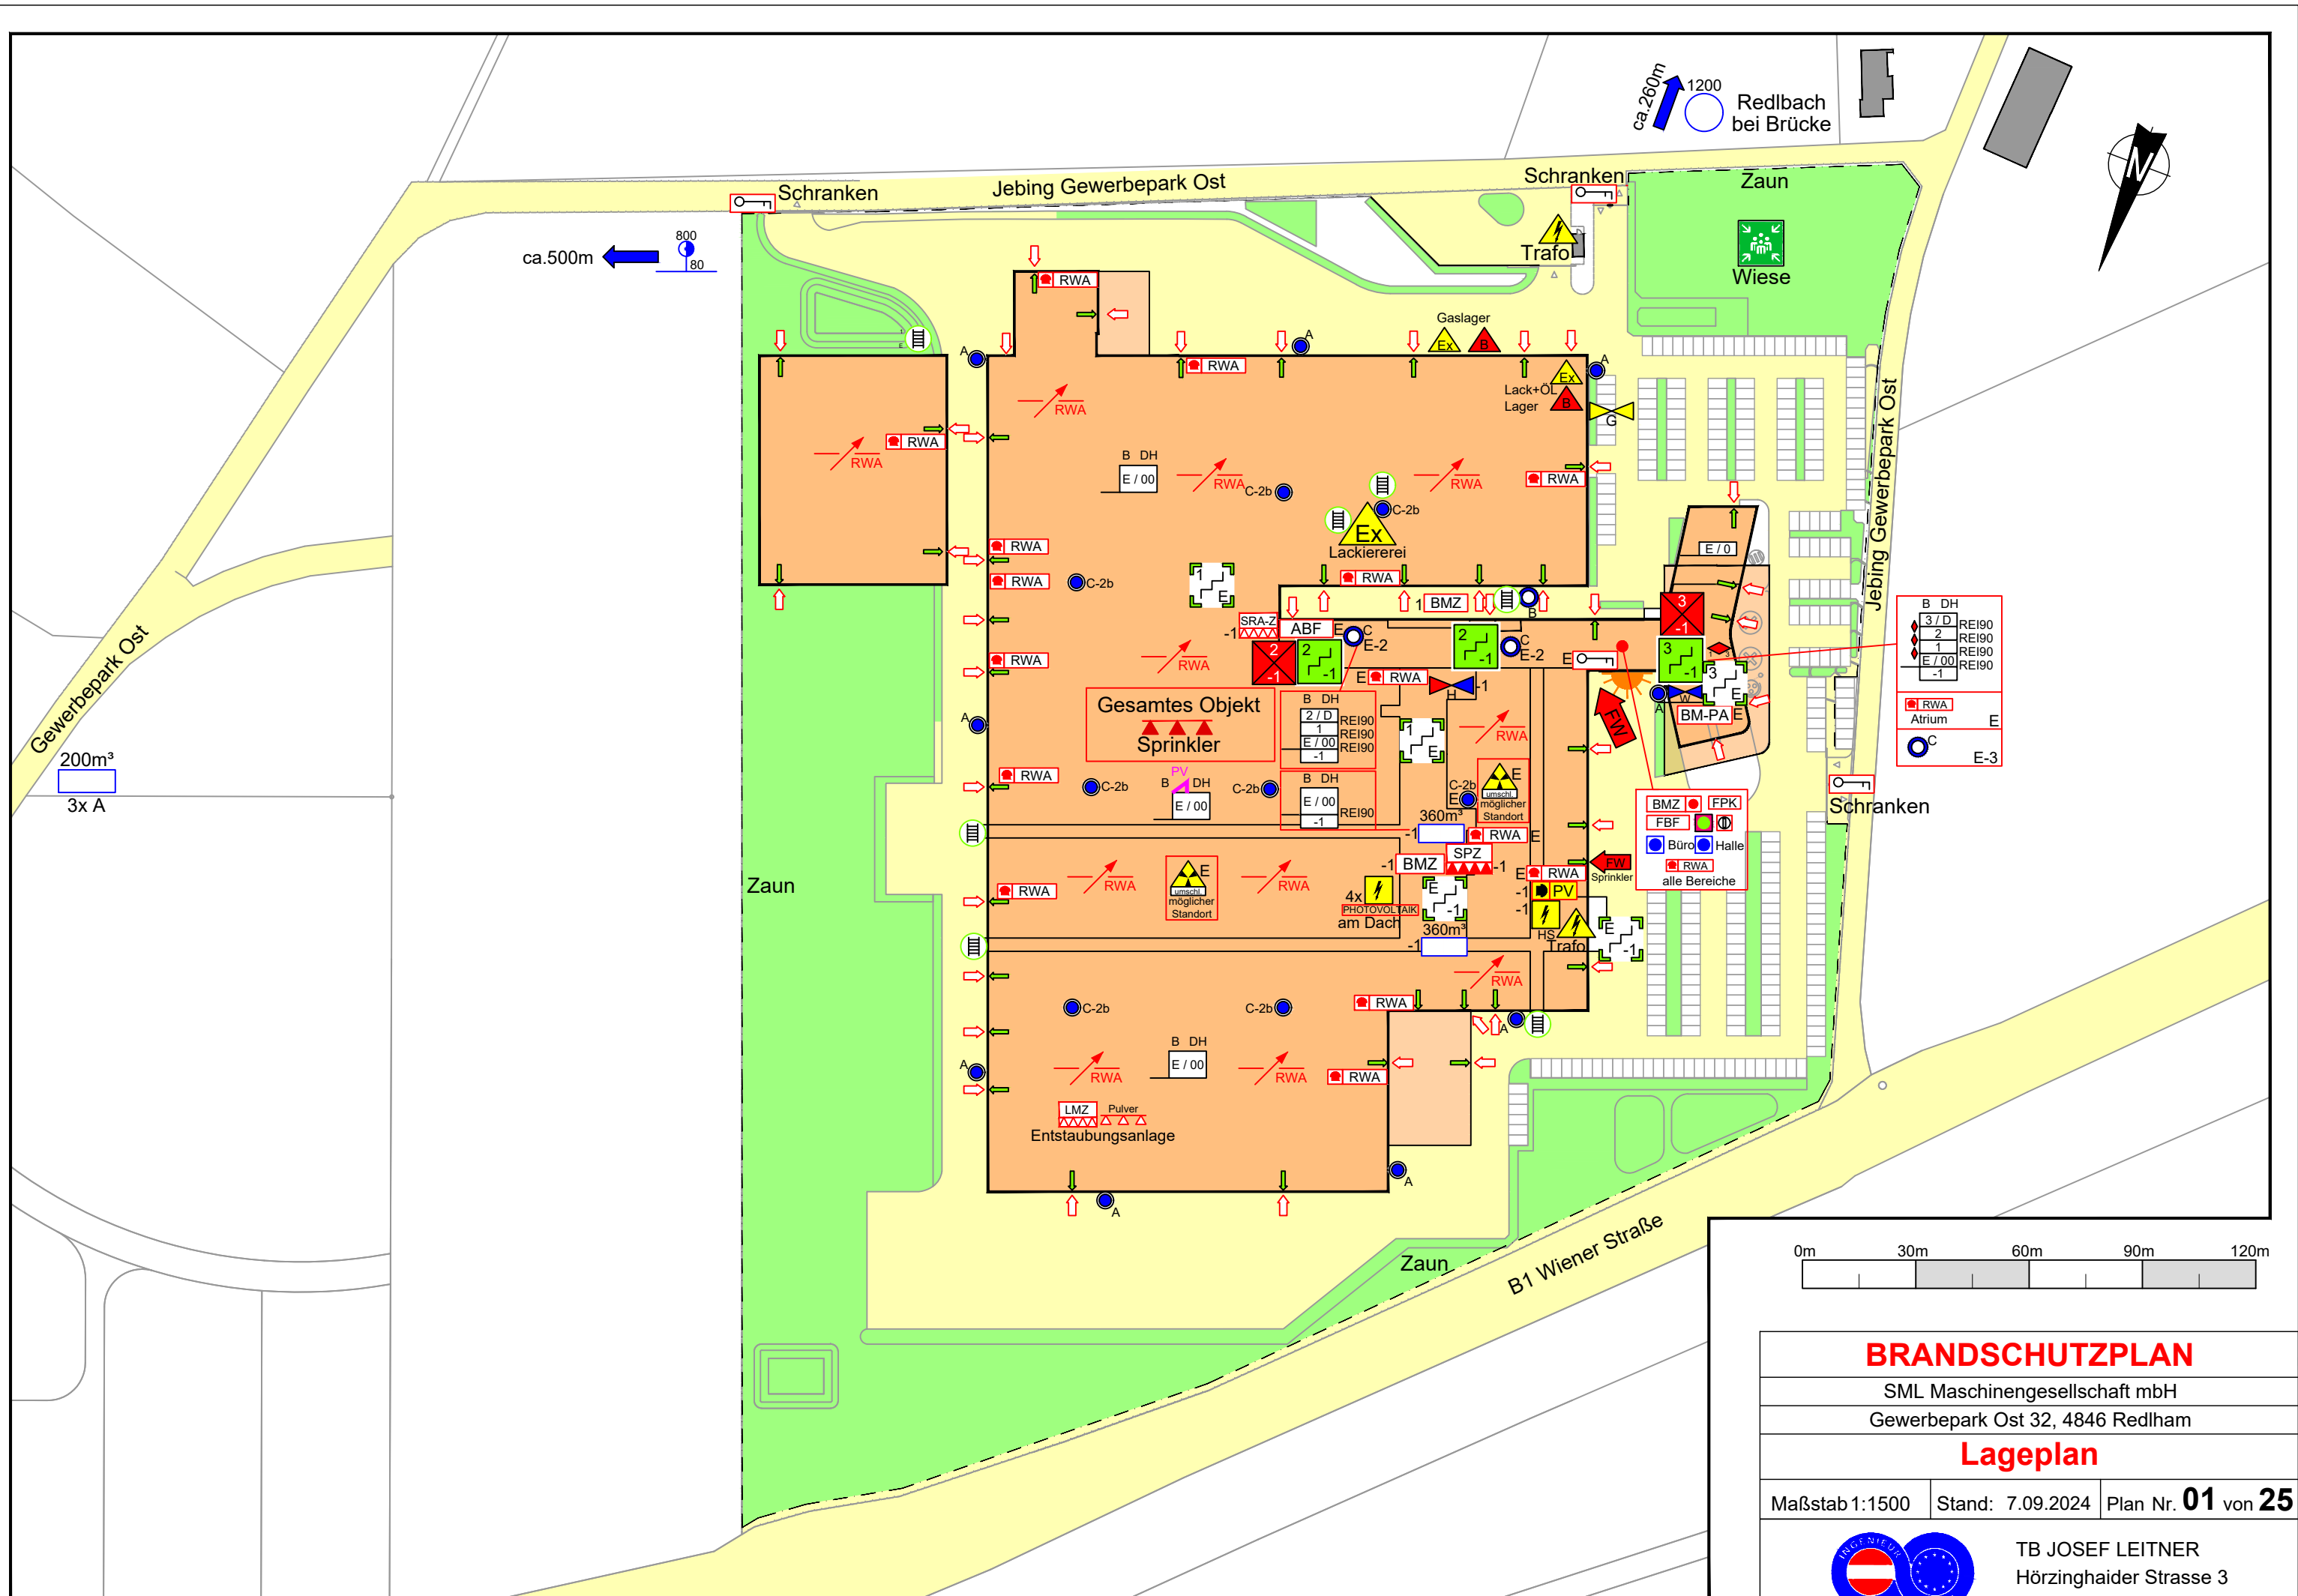


BRANDSCHUTZPLAN


SML Maschinengesellschaft mbH
Gewerbepark Ost 32, 4846 Redlham

Lageplan

Maßstab 1:1500 | Stand: 7.09.2024 | Plan Nr. **01** von **25**

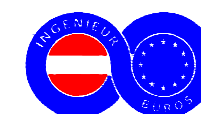

TB JOSEF LEITNER
Hörzinghaider Strasse 3
A - 4623 Gunskirchen

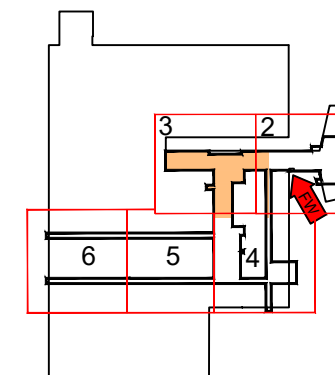


	2 / D
	1
	E / 00
	K / -0



911	921	9901
-----	-----	------

912	914	916	917	918	922
923	924	925	926	927	2912
9902	9906				

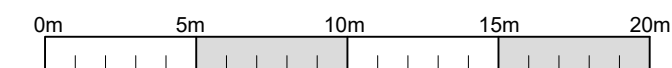

BRANDSCHUTZPLAN

Gewerbepark Ost 32, 4846 Redlham

UNTERGESCHOSS

Maßstab 1:250

Stand: 7.09.2024



4 Plan Nr. **03** von **25**



TB JOSEF LEITNER
Hörzinghaider Strasse 3
A - 4623 Gunskirchen

Anschlussplan 04

Anschlussplan 02

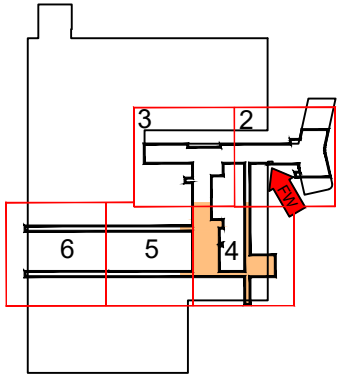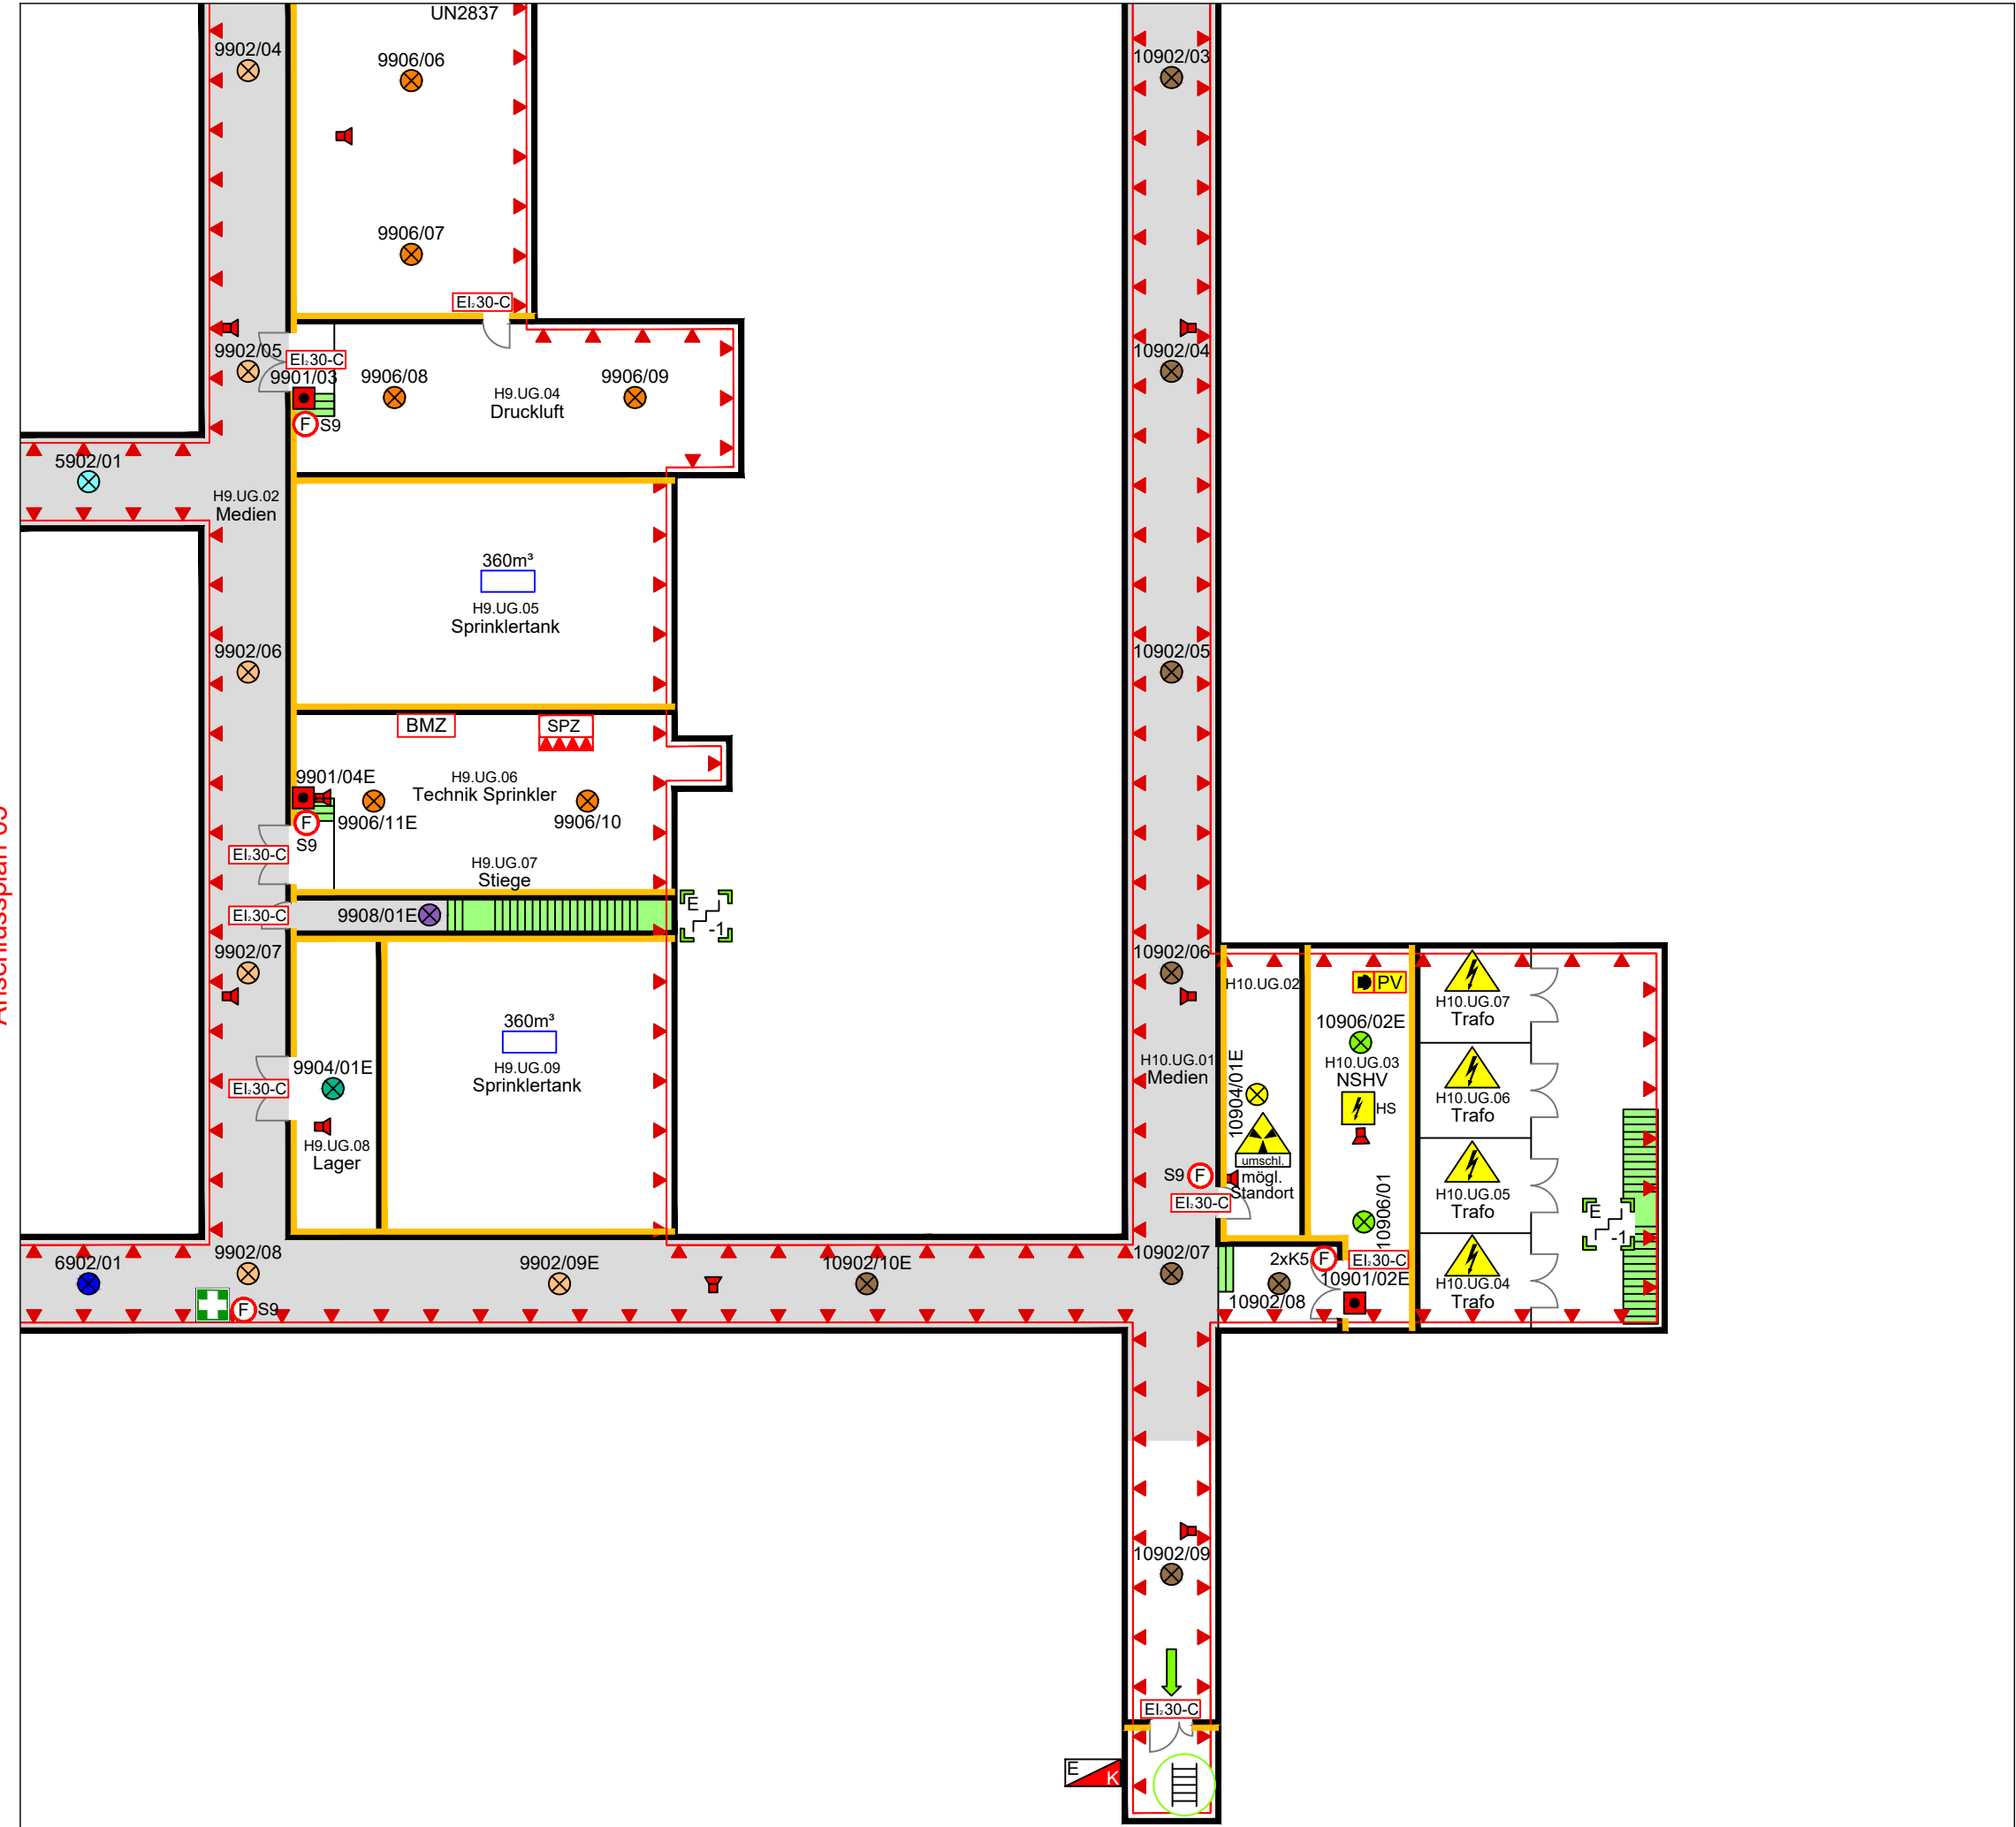

Übersichtsplan




1 / DG
E / 00
K / -01

BRANDMELDEGRUPPEN:
DRUCKKNOPFMELDER:

9901 10901

BRANDMELDER:

5902 6902 9902 9904 9906 9908
10902 10904 10906

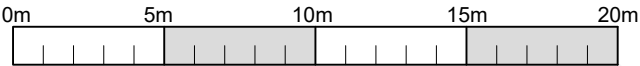


BRANDSCHUTZPLAN

SML Maschinengesellschaft mbH
Gewerbepark Ost 32, 4846 Redlham



UNTERGESCHOSS

Maßstab 1:250 Stand: 7.09.2024 Plan Nr. 04 von 25

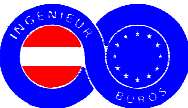

TB JOSEF LEITNER
Hörzinghaider Strasse 3
A - 4623 Gunskirchen

Anschlussplan 03

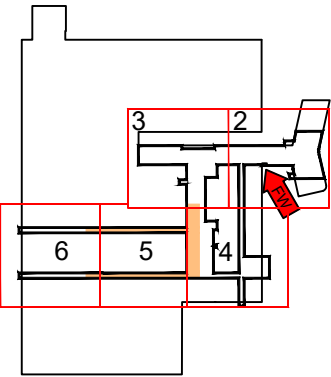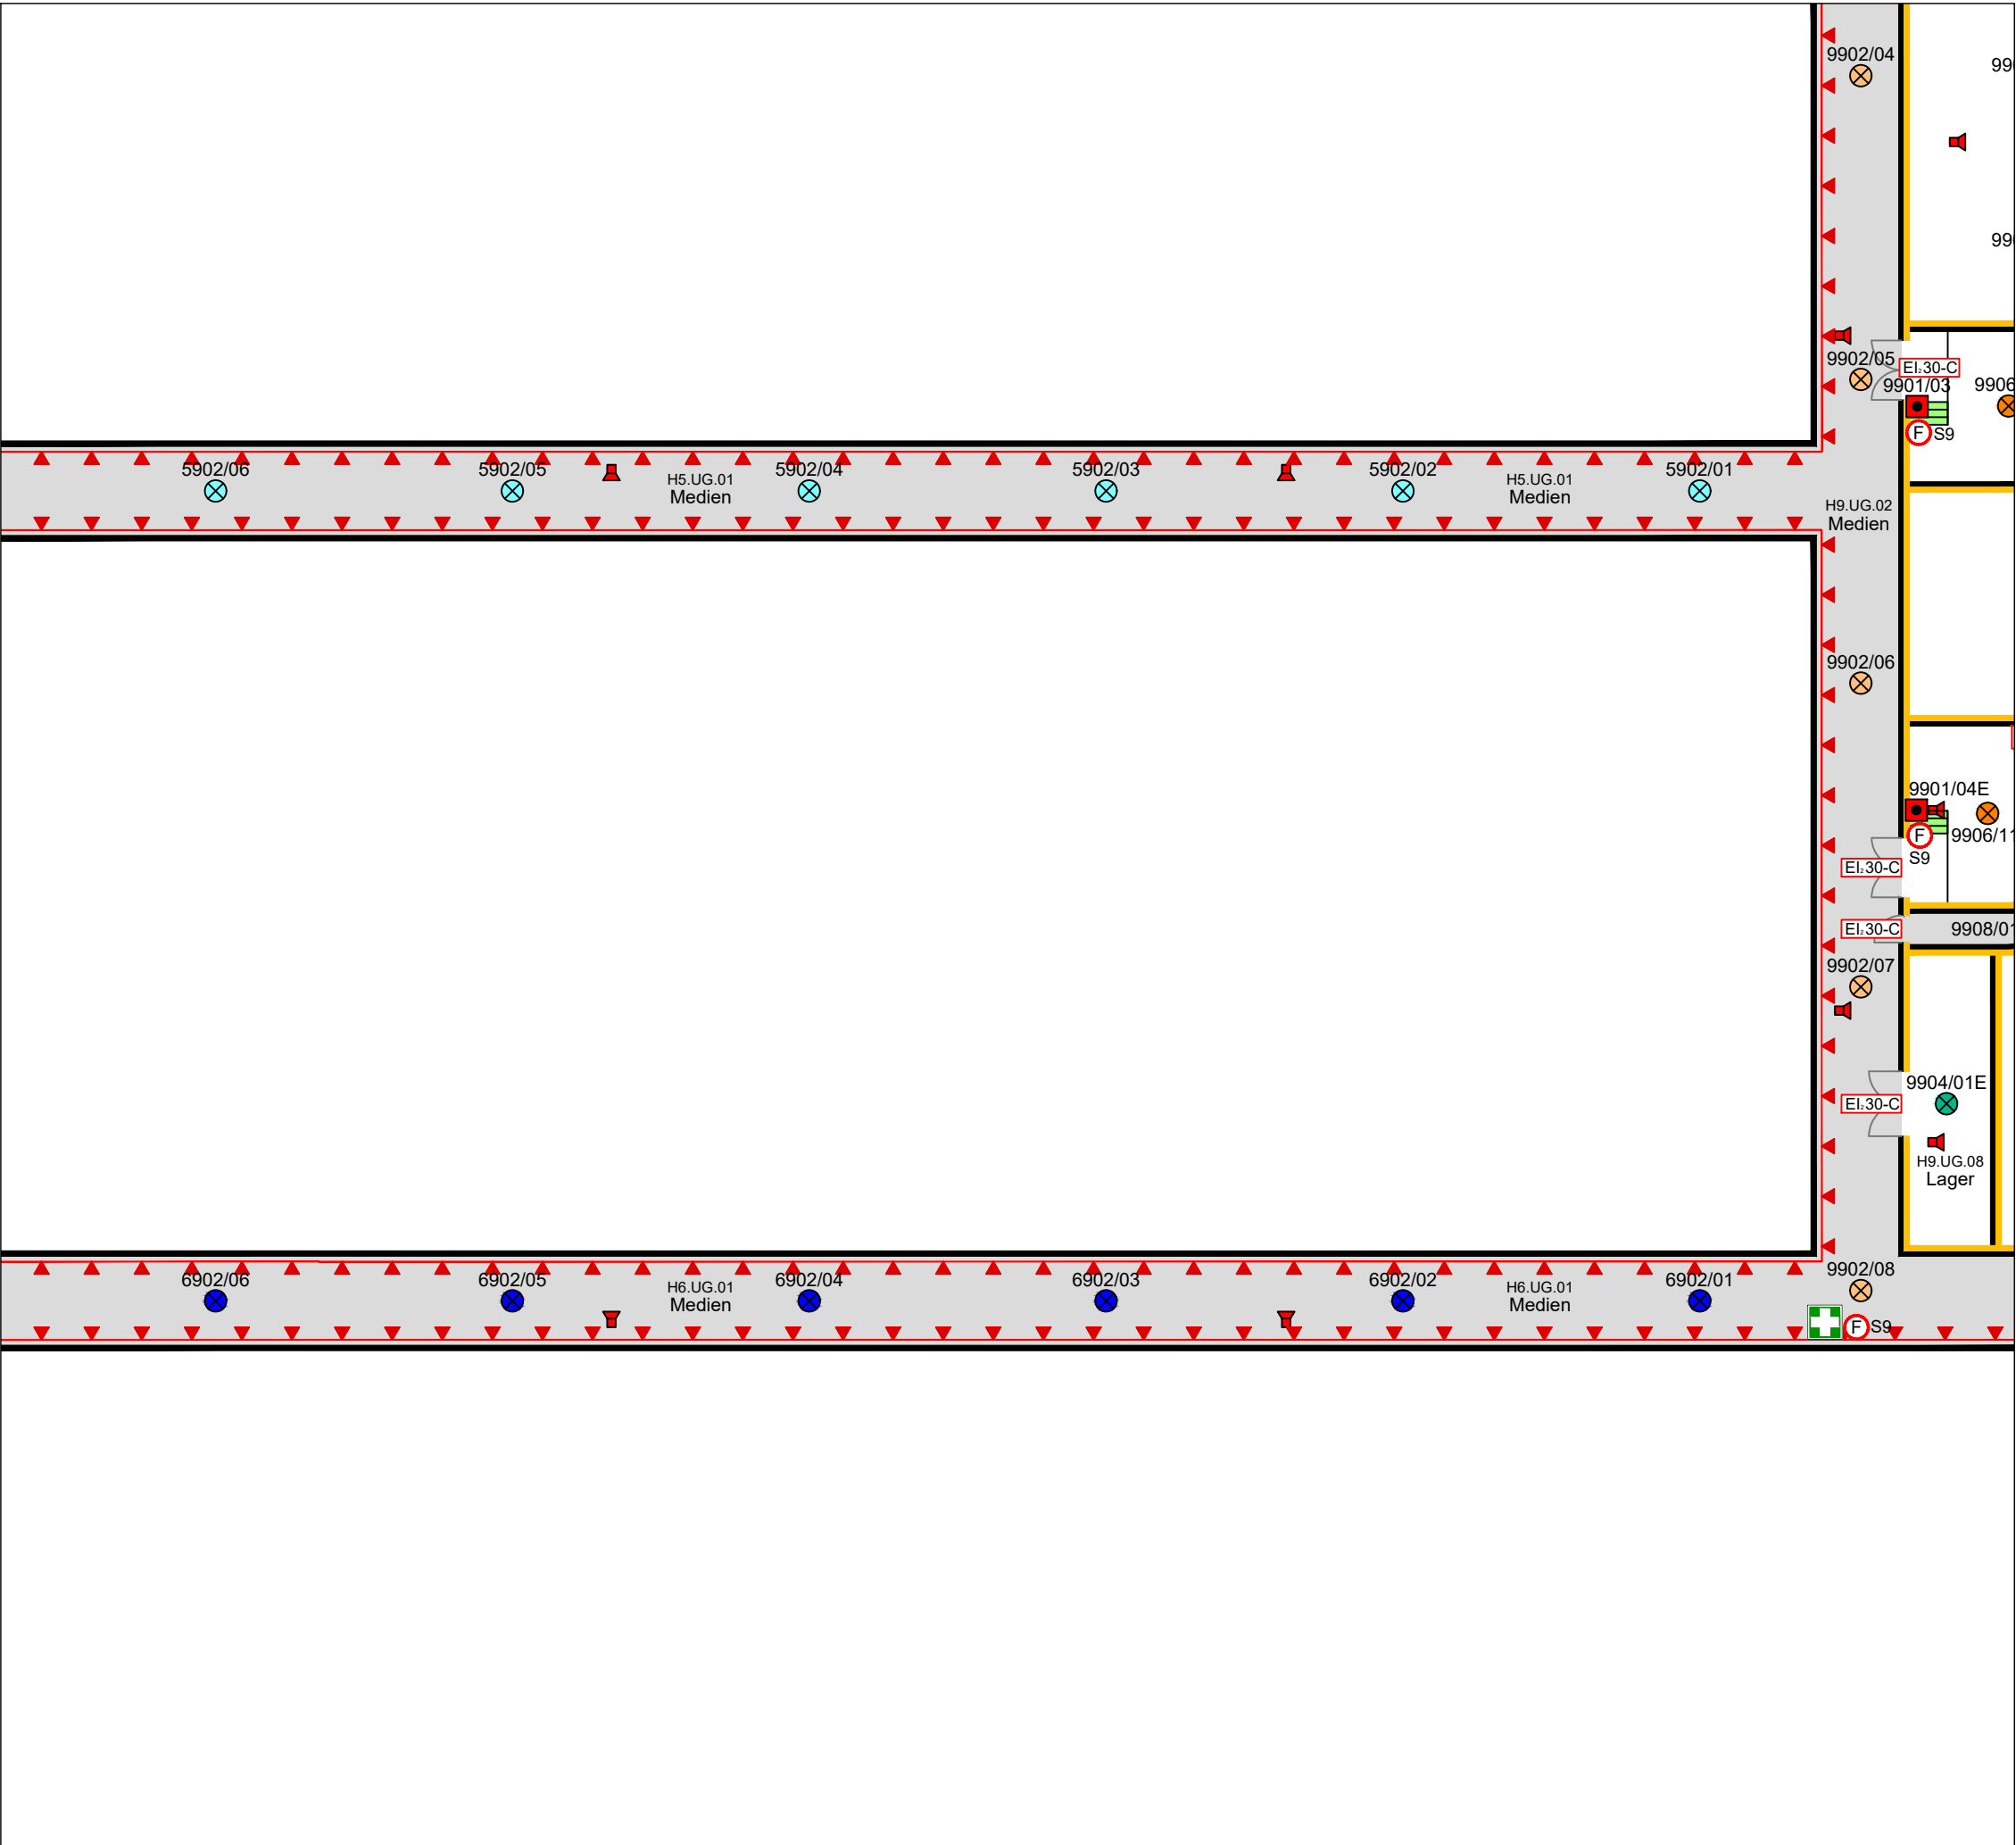

Übersichtsplan



E / 00
K / -01

BRANDMELDEGRUPPEN:
DRUCKKNOPFMELDER:

9901

BRANDMELDER:

5902 6902 9902 9904 9906




BRANDSCHUTZPLAN




SML Maschinengesellschaft mbH
Gewerbepark Ost 32, 4846 Redlham

UNTERGESCHOSS

Maßstab 1:250 | Stand: 7.09.2024 | Plan Nr. 05 von 25

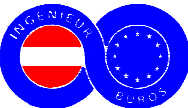

TB JOSEF LEITNER
Hörzinghaider Strasse 3
A - 4623 Gunskirchen

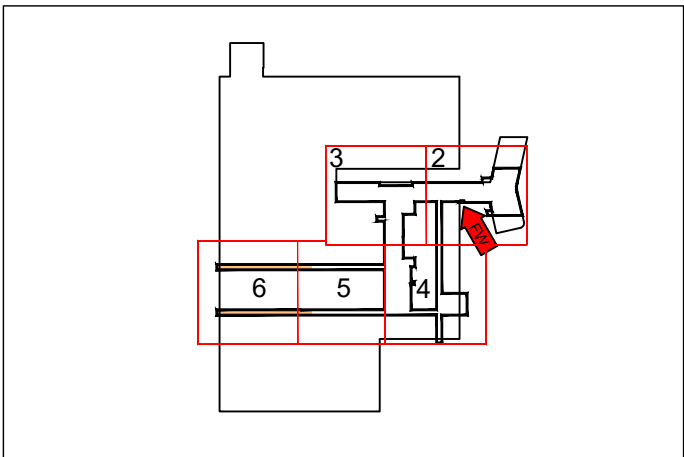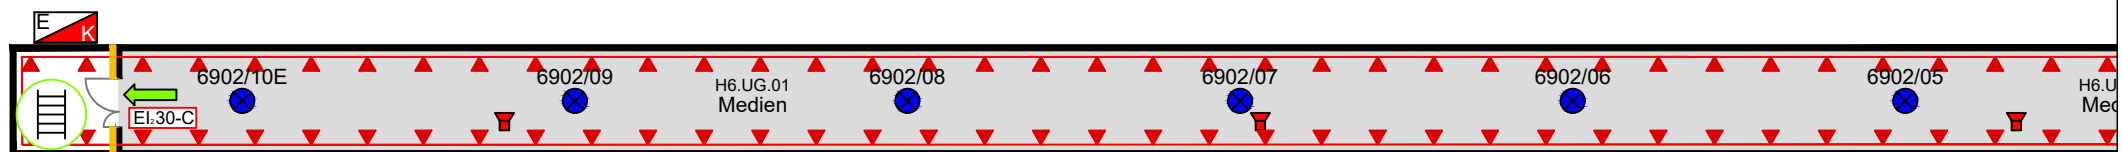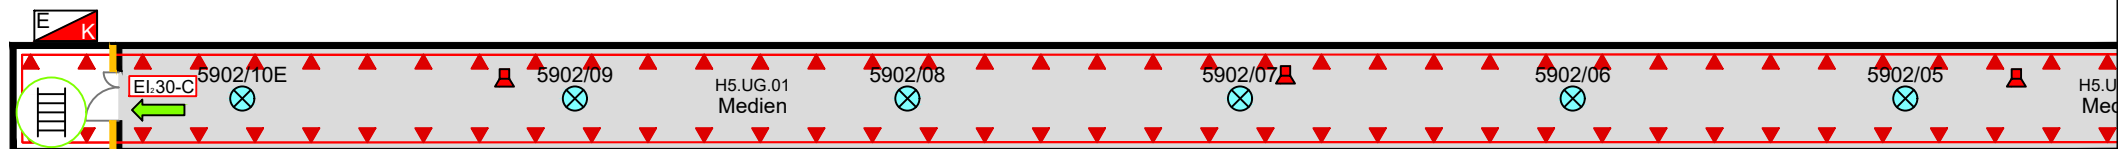

Übersichtsplan




Anschlussplan 05

1 / DG
E / 00
K / -01

BRANDMELDEGRUPPEN:
DRUCKKNOPFMELDER:

BRANDMELDER:

5902 6902

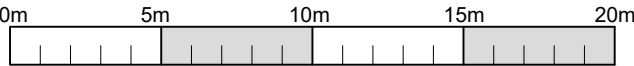


BRANDSCHUTZPLAN

SML Maschinengesellschaft mbH
Gewerbepark Ost 32, 4846 Redlham

UNTERGESCHOSS

Maßstab 1:250 Stand: 7.09.2024 Plan Nr. **06** von **25**

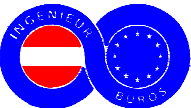


TB JOSEF LEITNER
Hörzinghaider Strasse 3
A - 4623 Gunskirchen

Anschlussplan 08



Anschlussplan 13

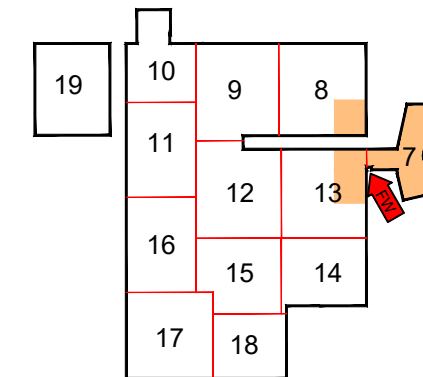

Übersichtsplan



3 / D
2
1
E / 00
K / -01

BRANDMELDEGRUPPEN:
DRUCKKNOPFMELDER:

01	10	11	2001	10001
----	----	----	------	-------

BRANDMELDER:

02	03	04	06	07	08
12	14	15	22	10012	10013
10014	2003				

STRÖMUNGSWÄCHTER:

20121



BRANDSCHUTZPLAN

SML Maschinengesellschaft mbH



Gewerbepark Ost 32, 4846 Redlham

ERDGESCHOSS


Maßstab 1:250 | Stand: 7.09.2024 | Plan Nr. **07** von **25**



TB JOSEF LEITNER
Hörzinghaider Strasse 3
A - 4623 Gunskirchen

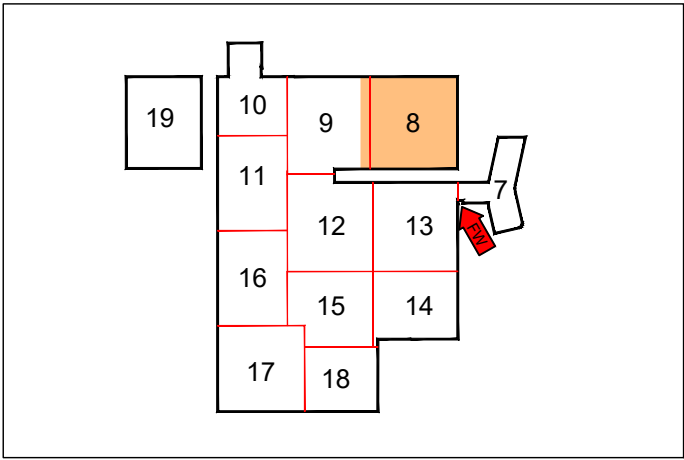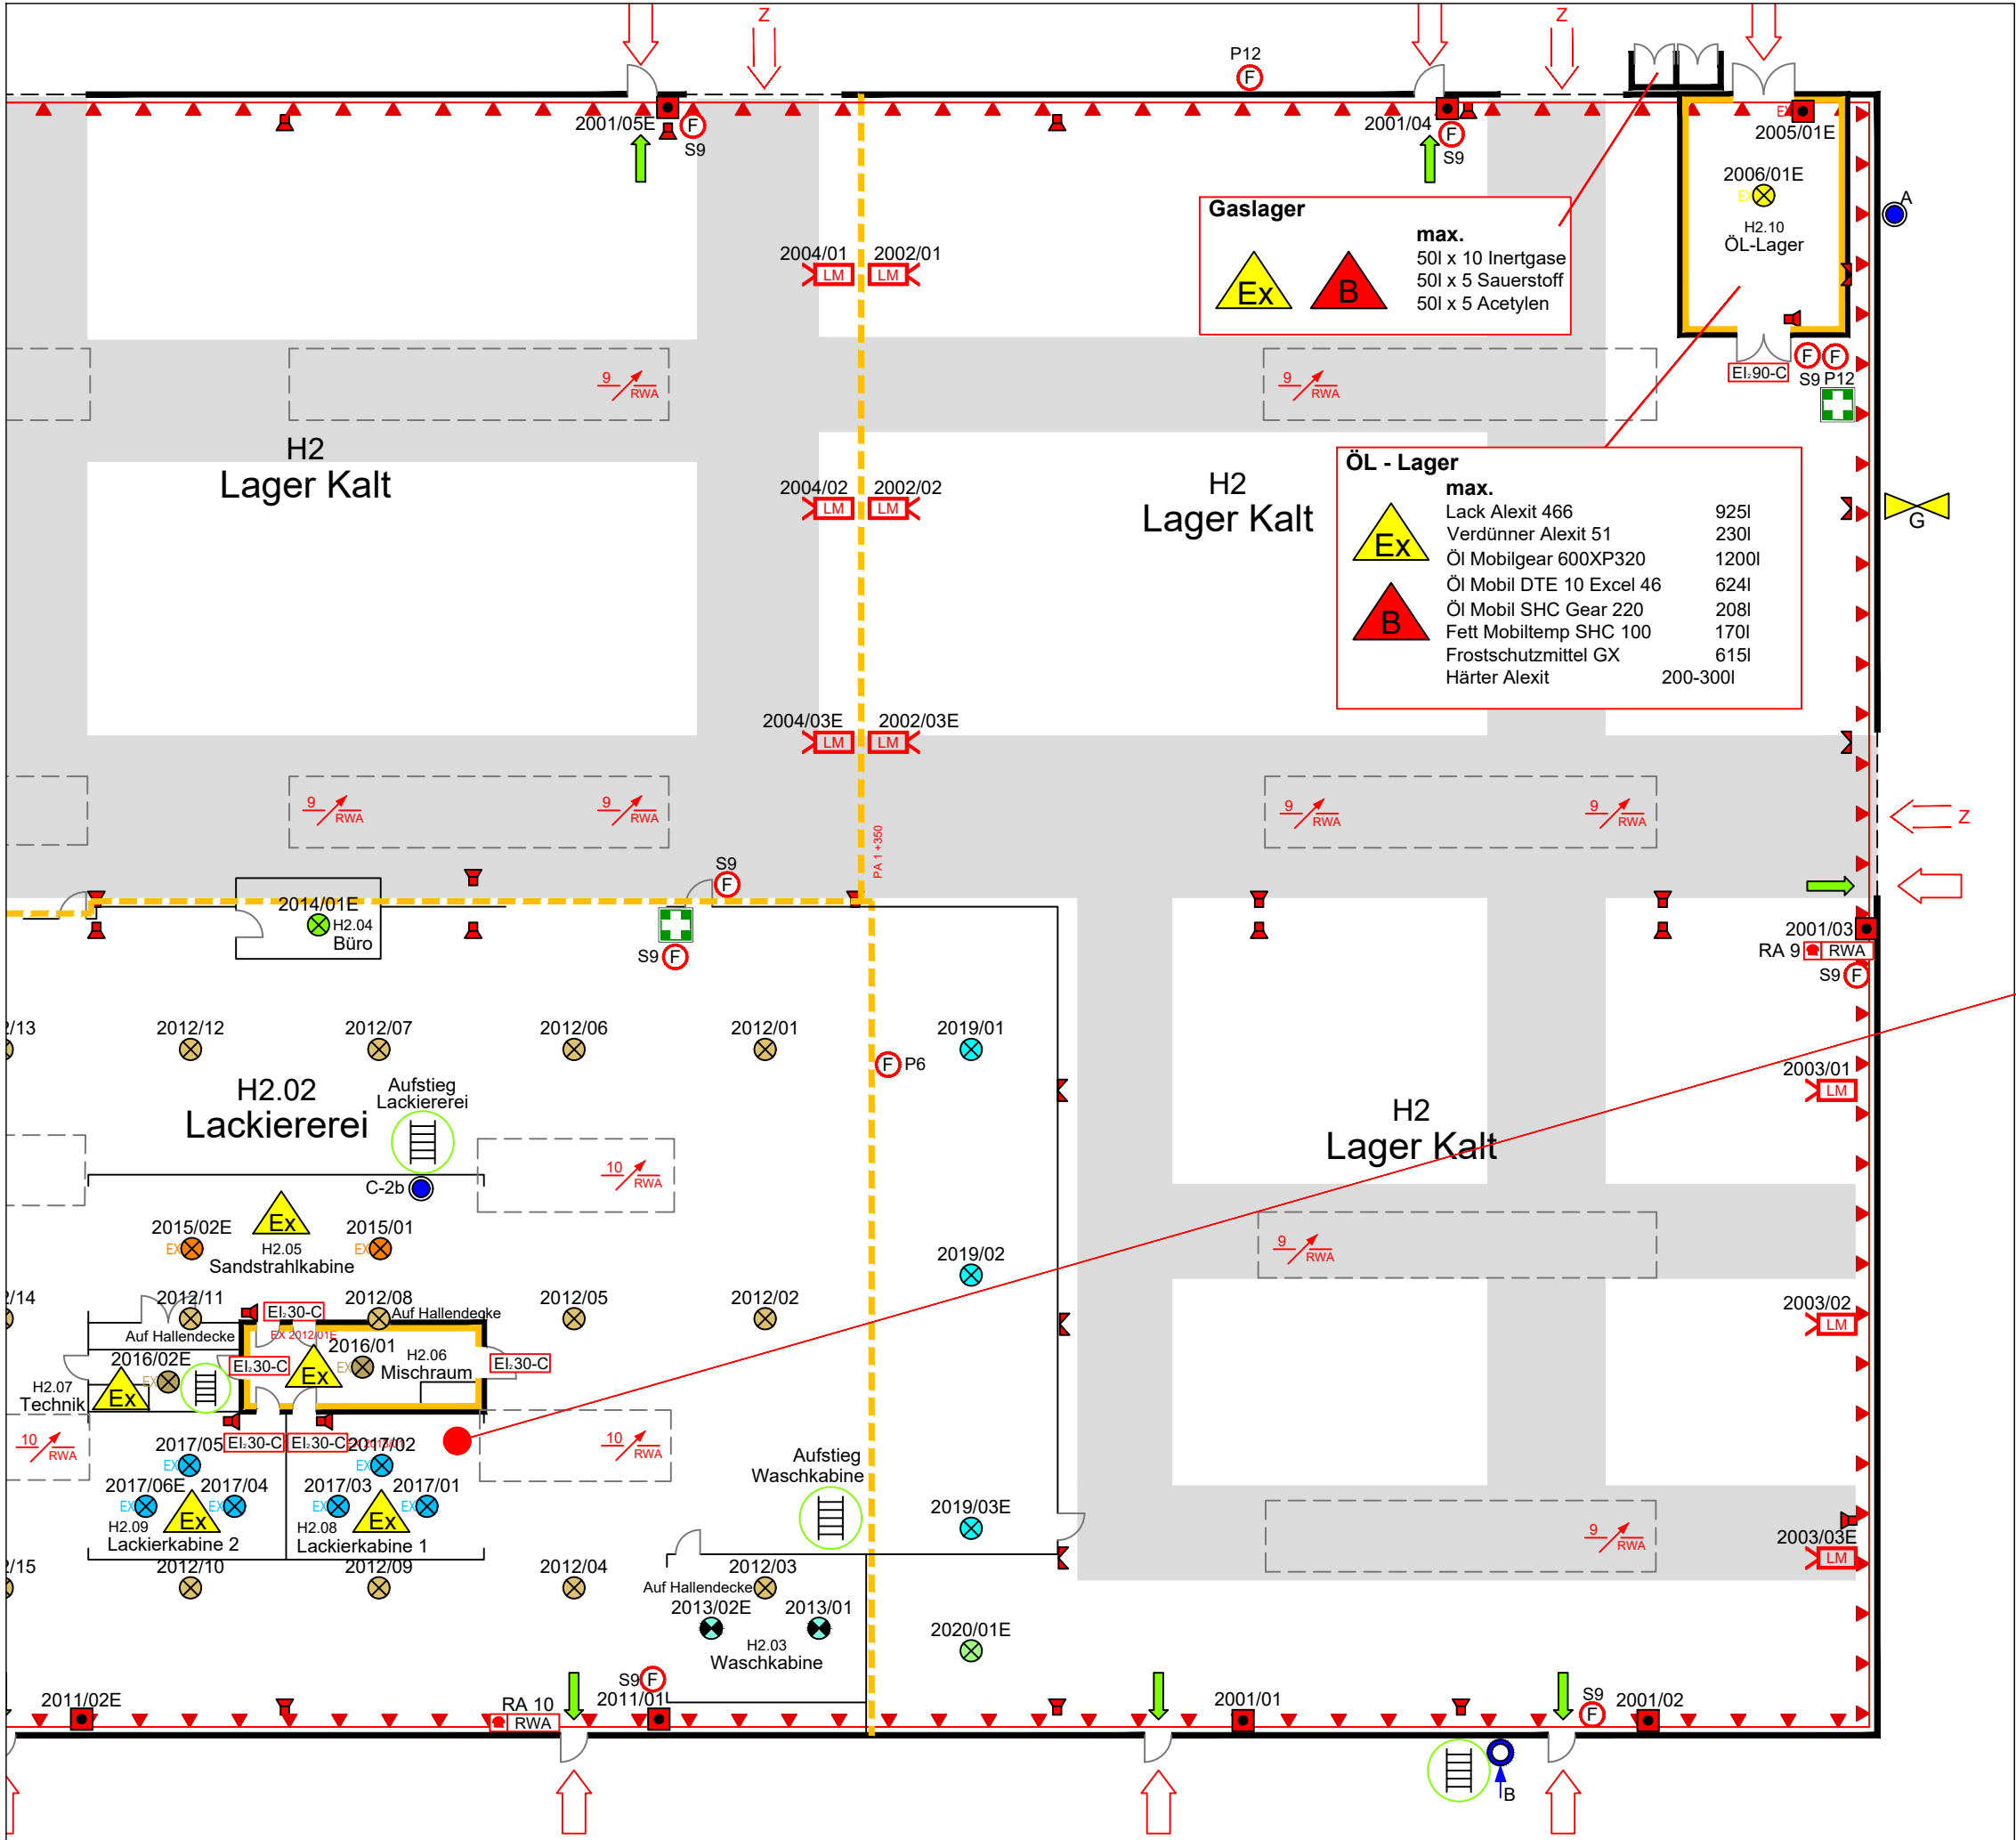

Übersichtsplan

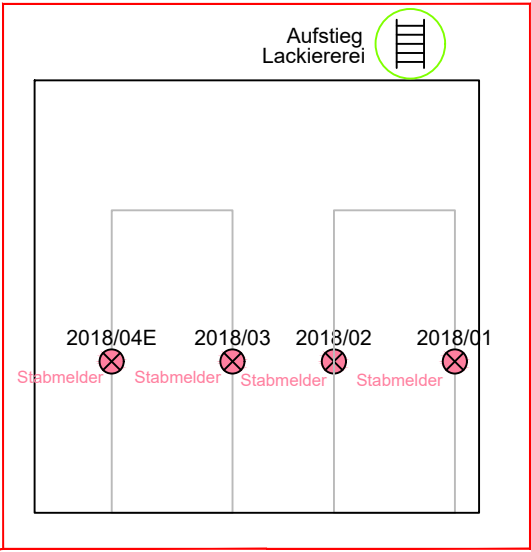

Detail 1 über Lackiererei


BRANDMELDEGRUPPEN: **E / 00**

DRUCKKNOPFMELDER:

2001 2005 2011

BRANDMELDER:

2002	2003	2004	2006	2012	2013
2014	2015	2016	2017	2018	2019
2020					

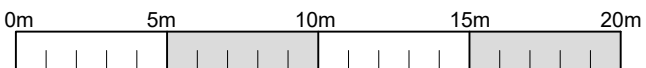

BRANDSCHUTZPLAN



SML Maschinengesellschaft mbH

Gewerbepark Ost 32, 4846 Redlham

ERDGESCHOSS

Maßstab 1:250 | Stand: 7.09.2024 | Plan Nr. **08** von **25**

TB JOSEF LEITNER
Hörzinghaider Strasse 3
A - 4623 Gunskirchen

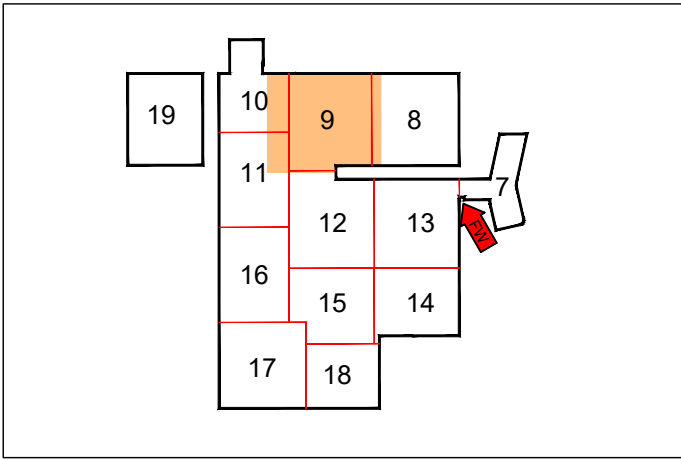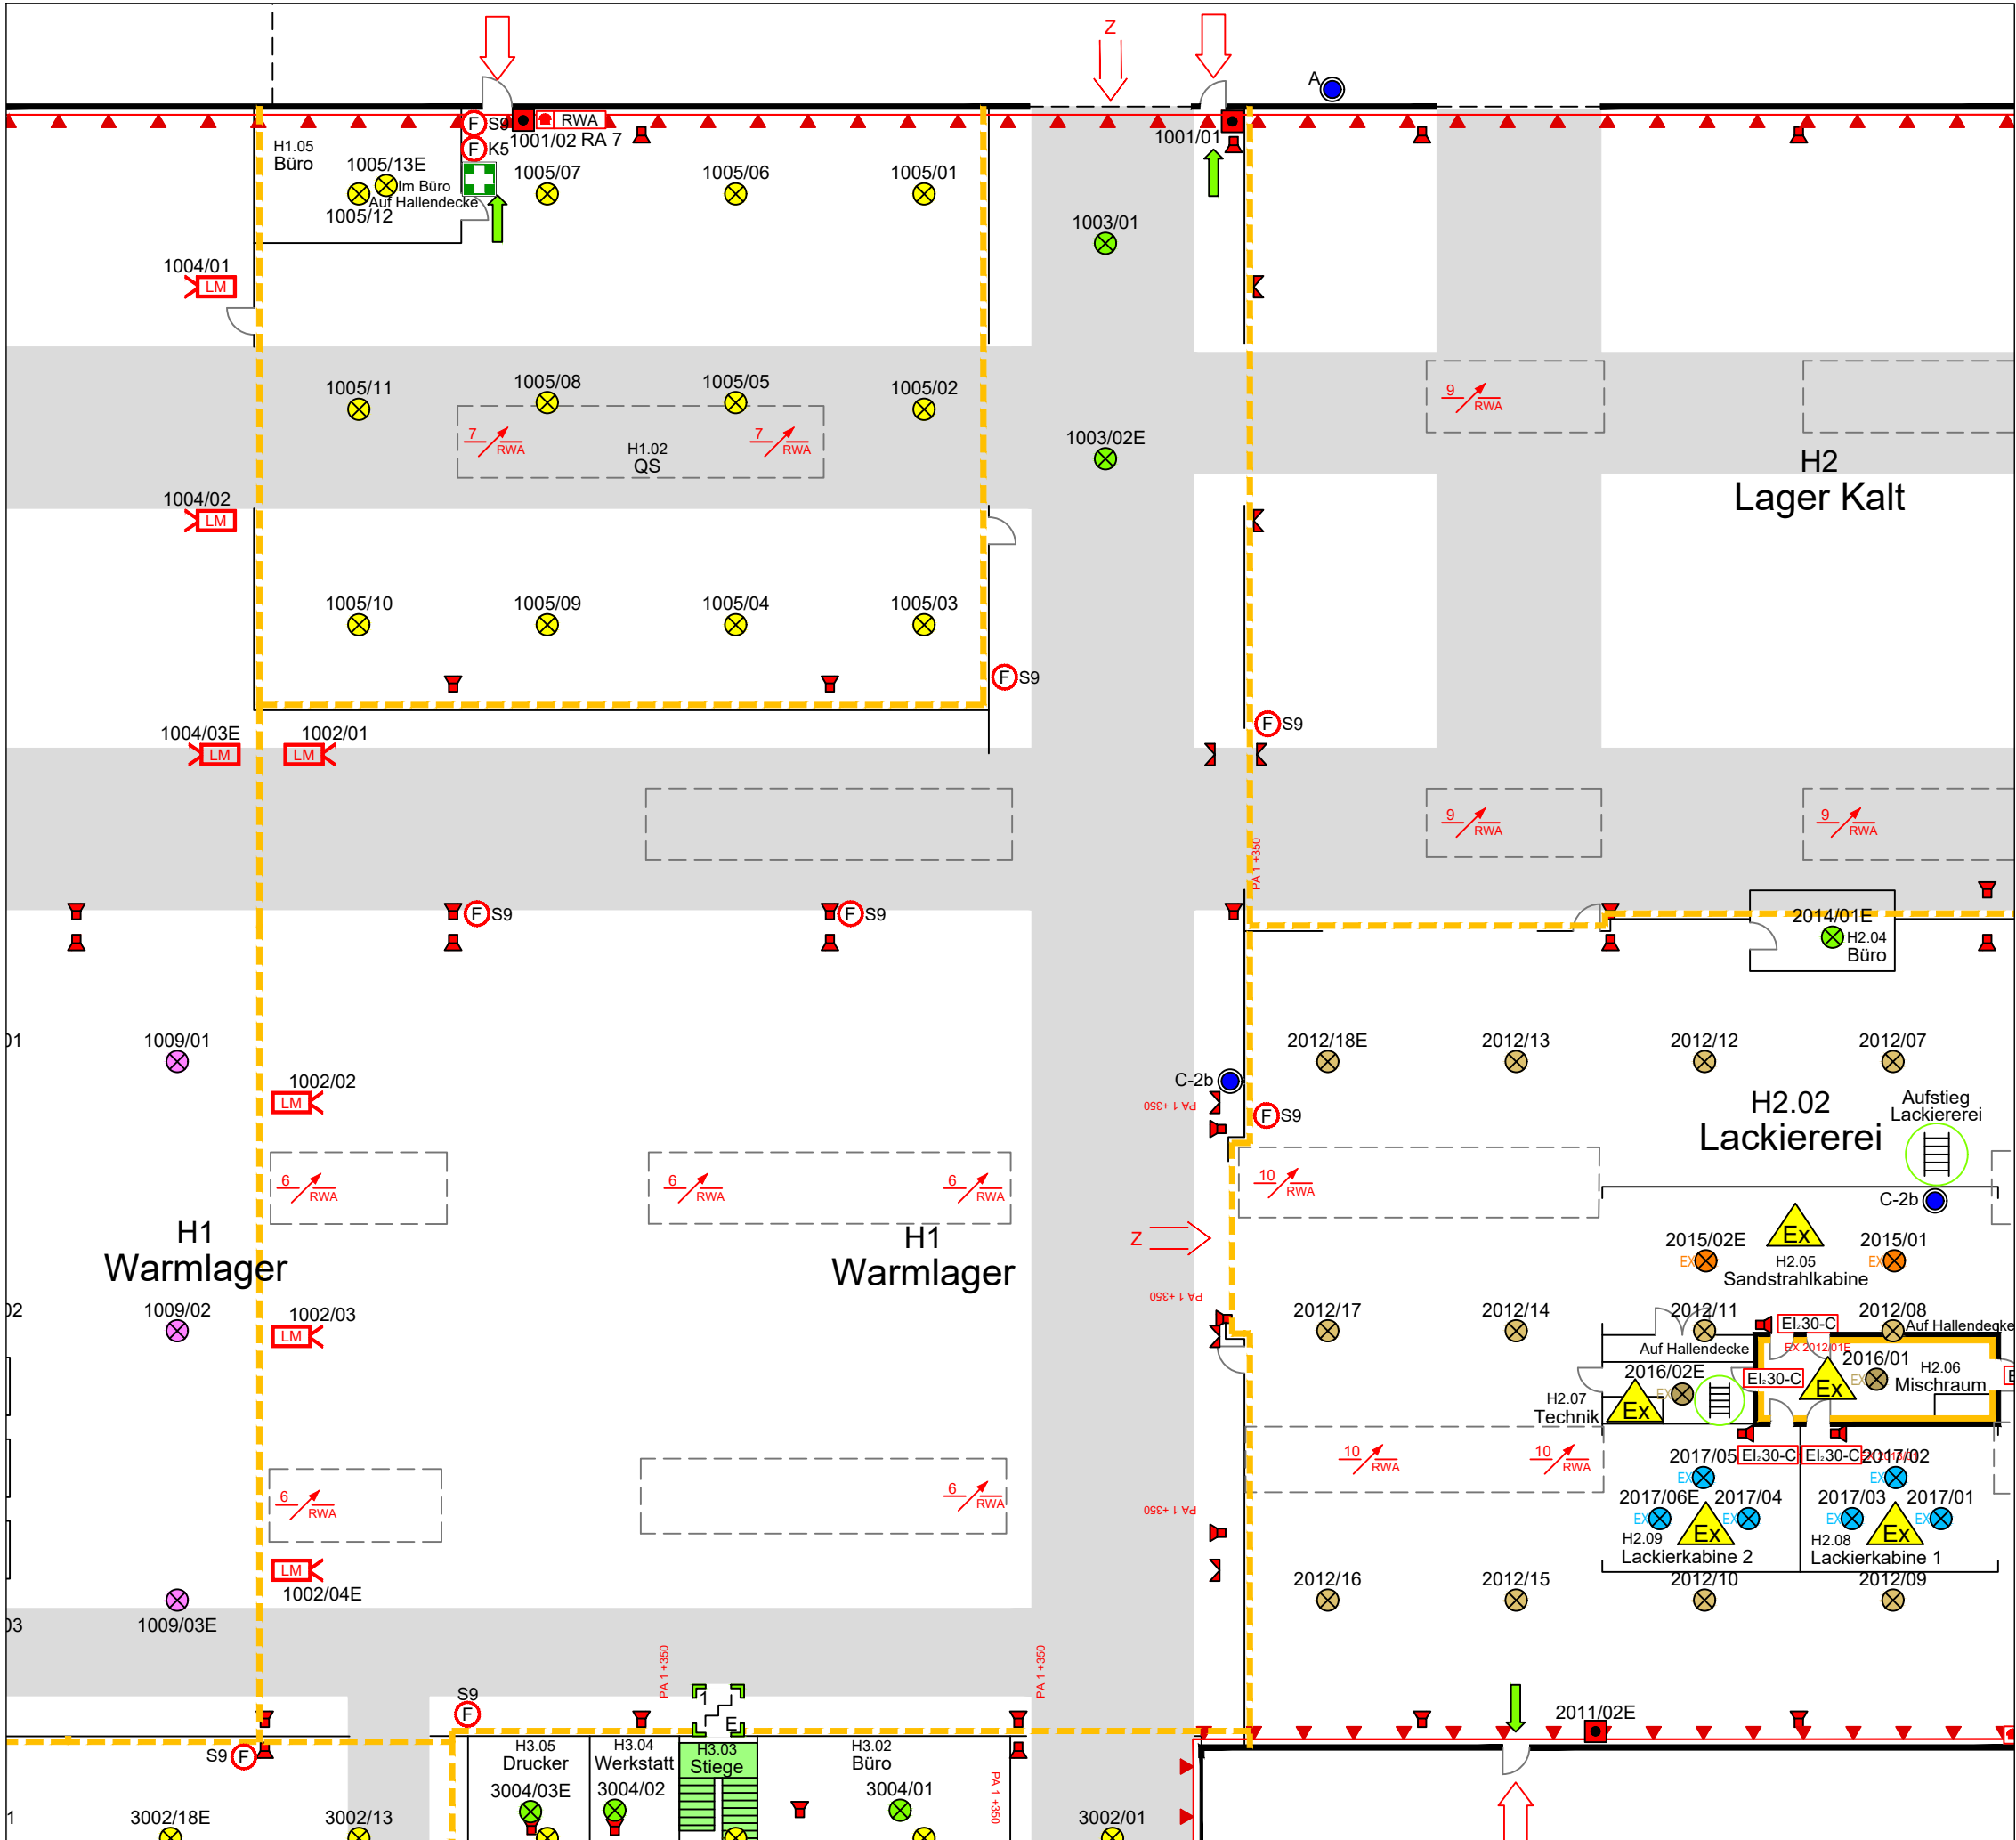

Übersichtsplan



E / 00

BRANDMELDEGRUPPEN:
DRUCKKNOPFMELDER:

1001 2011

BRANDMELDER:

1002	1003	1004	1005	2012	2015
2016	2017	3002	3003	3004	



BRANDSCHUTZPLAN



SML Maschinengesellschaft mbH
Gewerbepark Ost 32, 4846 Redlham

ERDGESCHOSS

Maßstab 1:250 Stand: 7.09.2024 Plan Nr. **09** von **25**



TB JOSEF LEITNER
Hörzinghaider Strasse 3
A - 4623 Gunskirchen

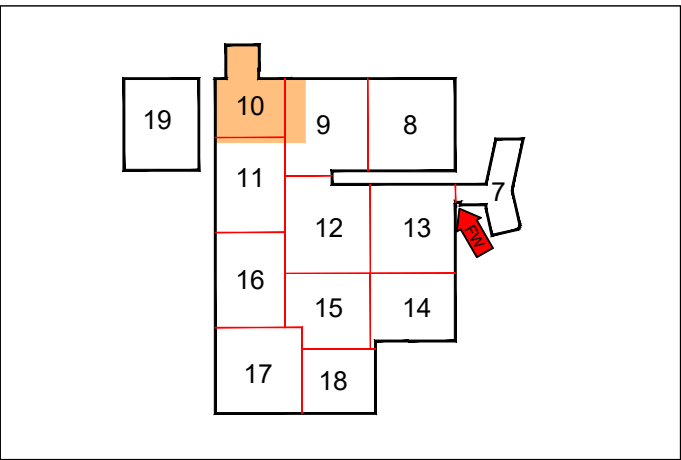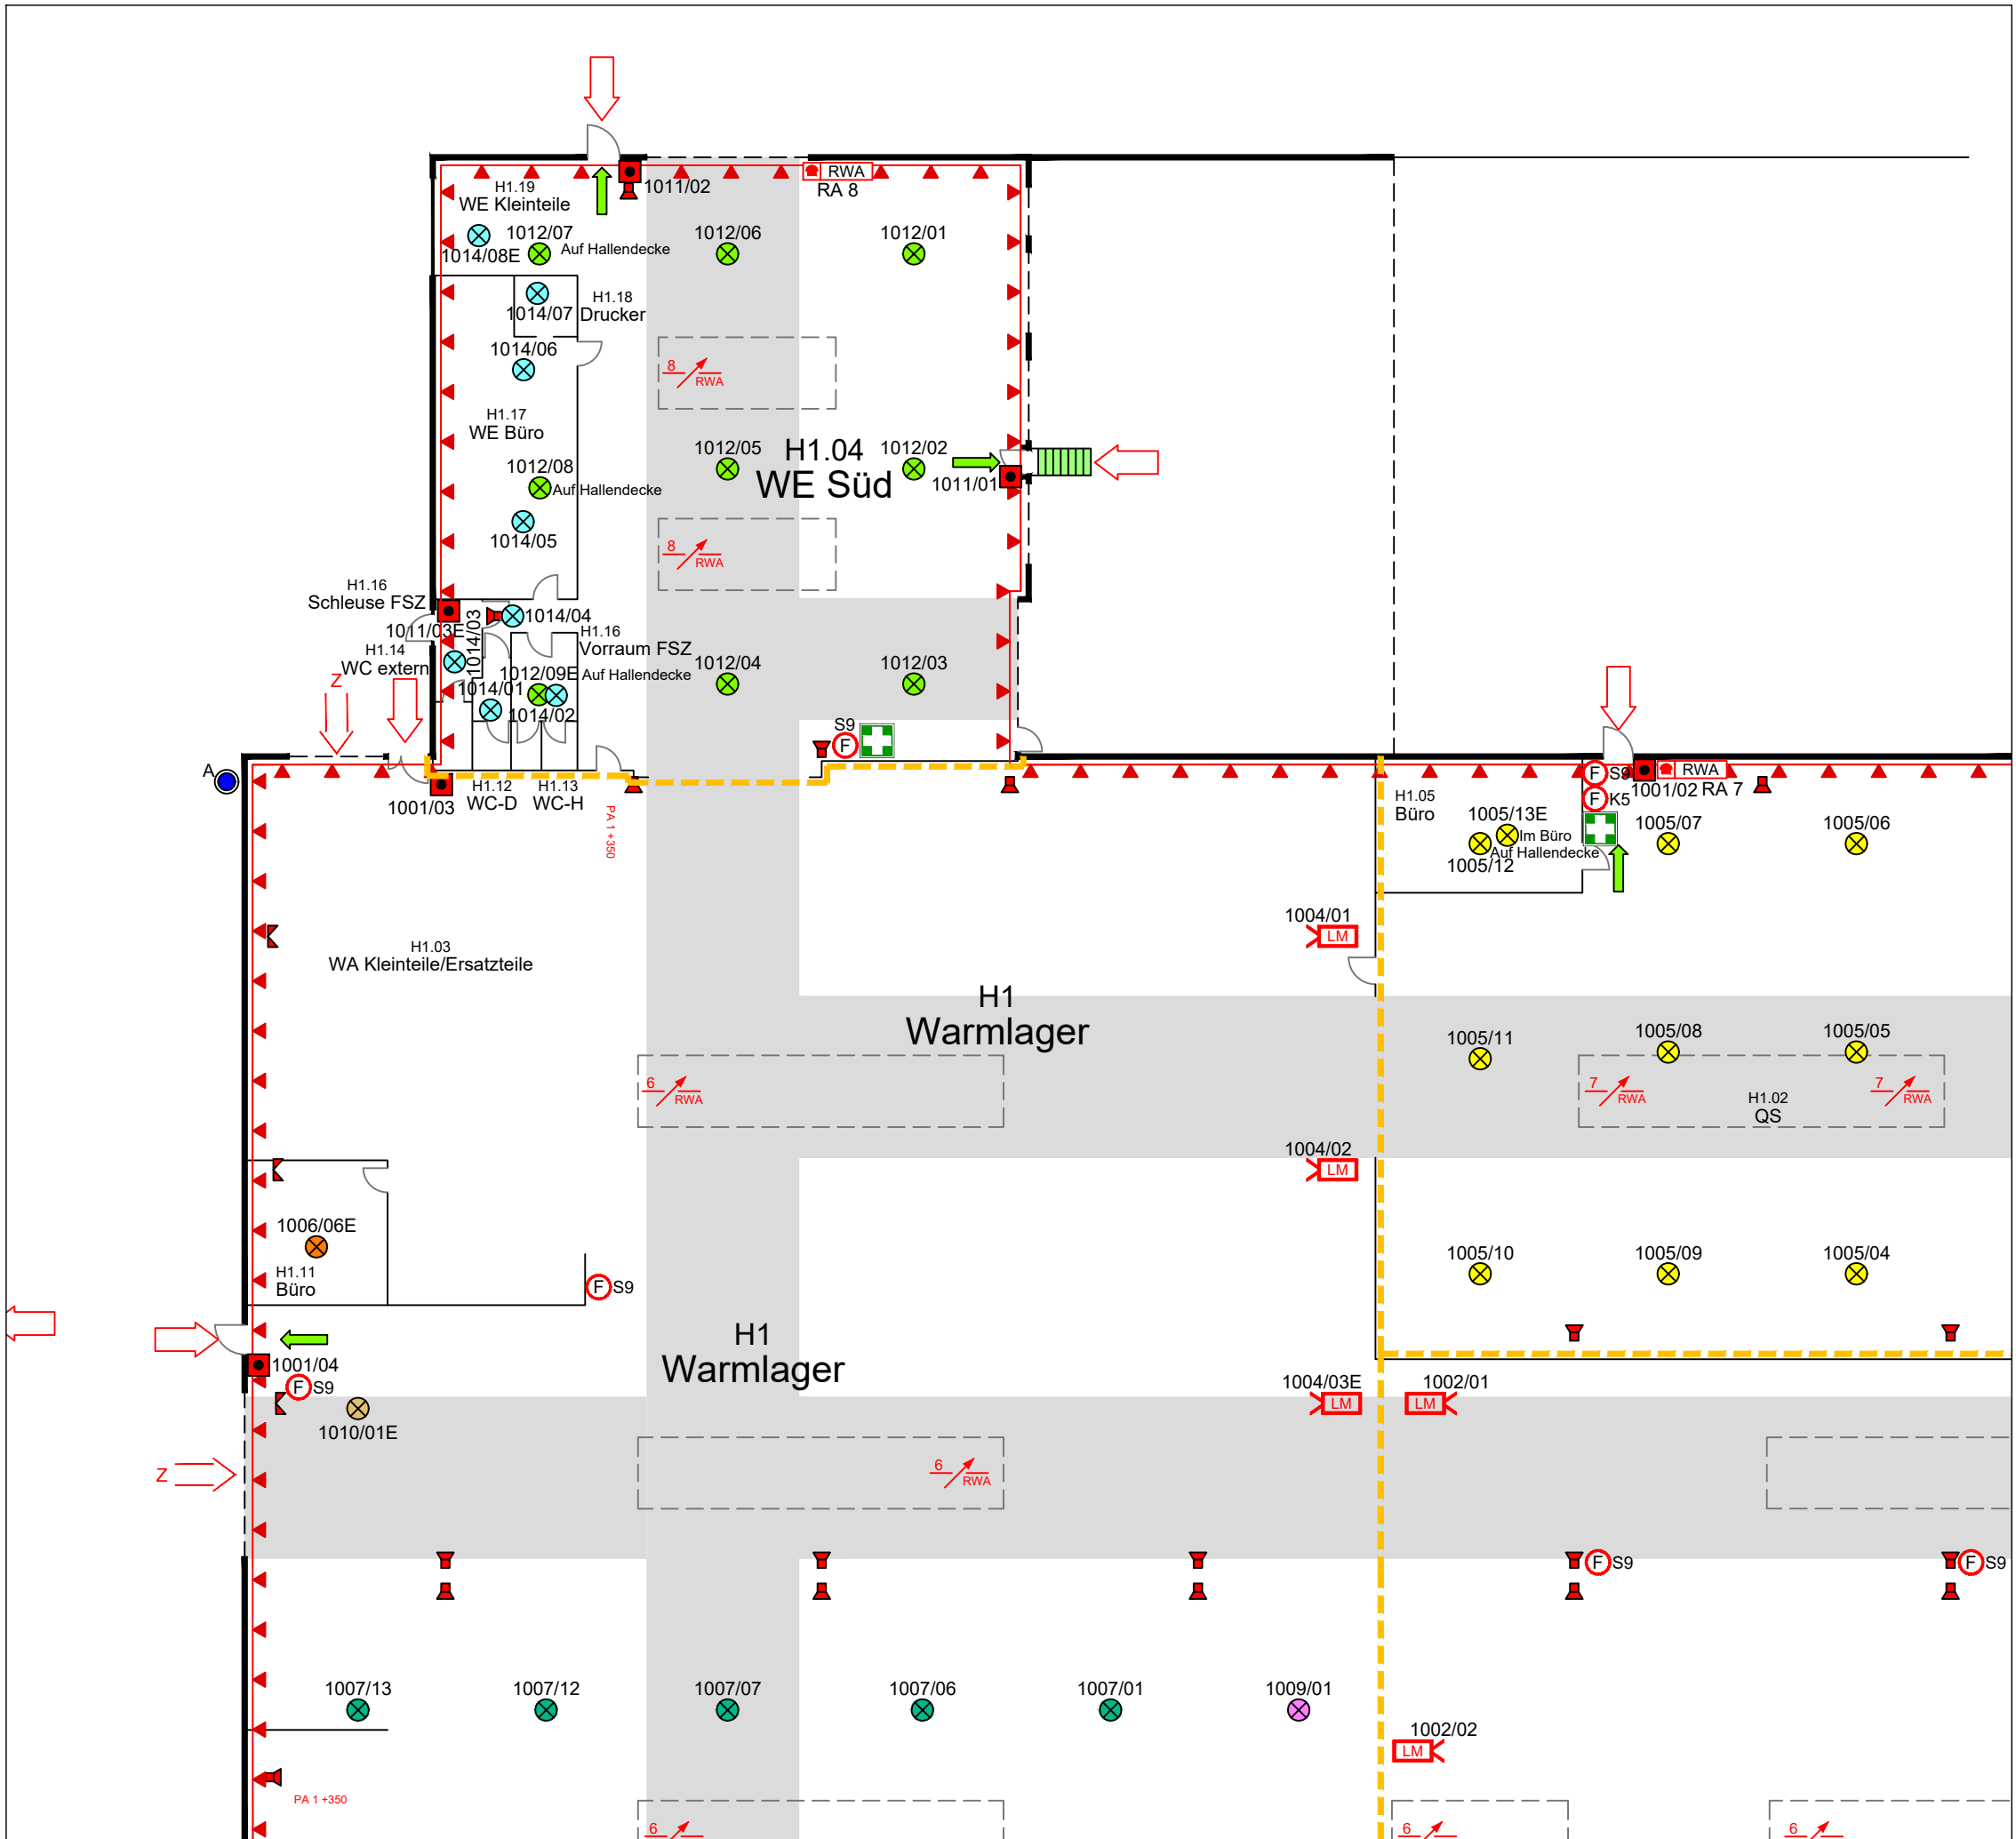

Übersichtsplan



1 / D
E / 00


Anschlussplan 09

BRANDMELDEGRUPPEN:
DRUCKKNOPFMELDER:

1001 1011

BRANDMELDER:

1002 1004 1005 1006 1007 1009
1010 1012 1014

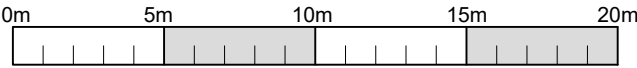


BRANDSCHUTZPLAN

SML Maschinengesellschaft mbH
Gewerbepark Ost 32, 4846 Redlham

ERDGESCHOSS


Maßstab 1:250 Stand: 7.09.2024 Plan Nr. **10** von **25**

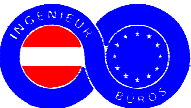


TB JOSEF LEITNER
Hörzinghaider Strasse 3
A - 4623 Gunskirchen

Anschlussplan 11

Anschlussplan 10

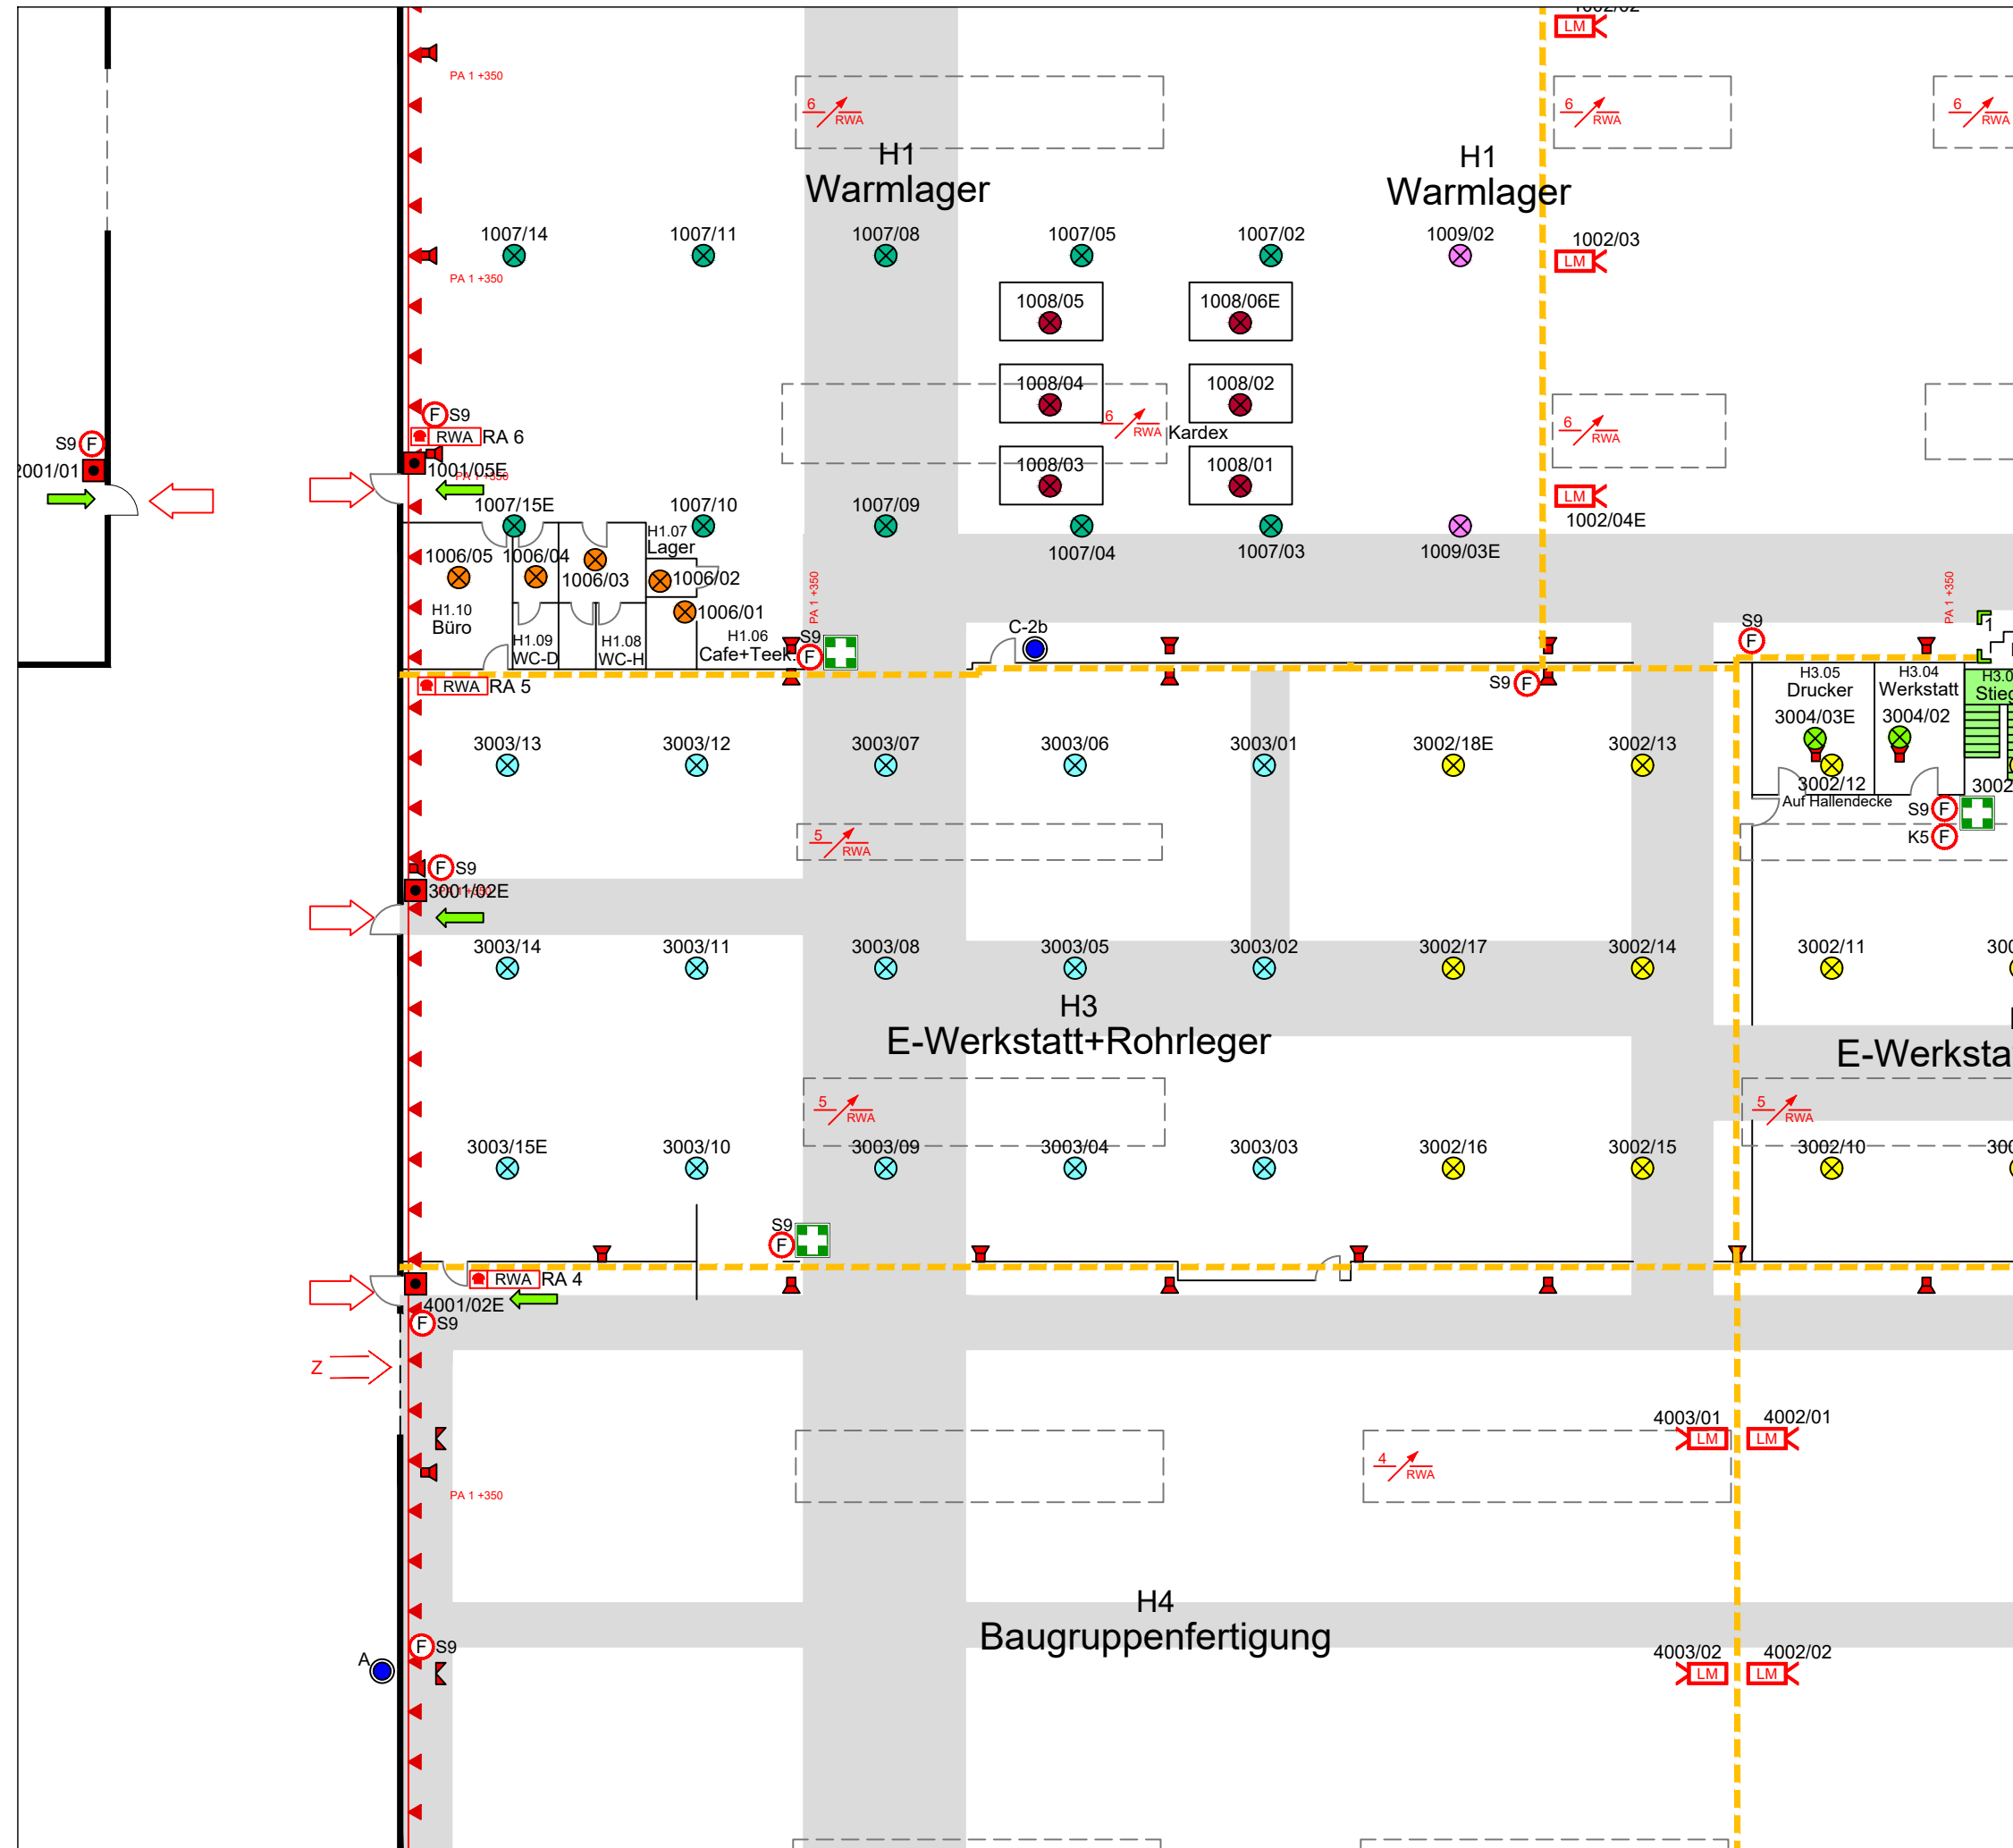

Anschlussplan 16

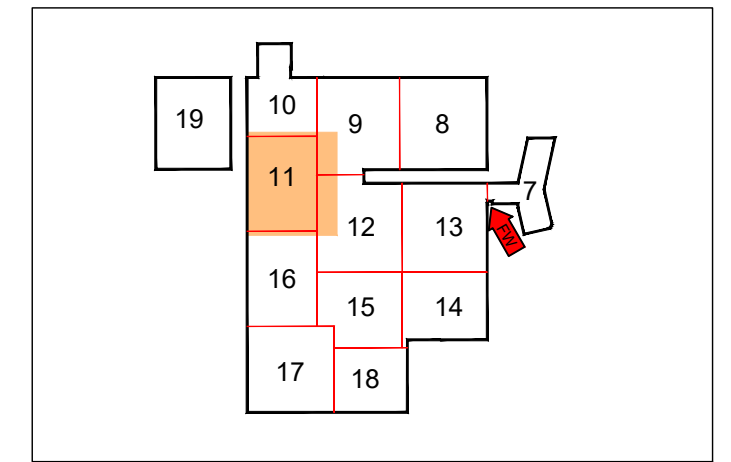

Übersichtsplan



1 / D
E / 00
K / -01


Anschlussplan 12

BRANDMELDEGRUPPEN:
DRUCKKNOPFMELDER:

1001 3001 4001

BRANDMELDER:

1002 1006 1007 1008 1009 3002
3003 3004 4002 4003

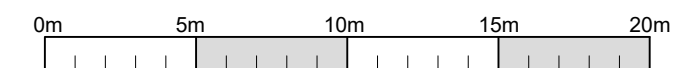

BRANDSCHUTZPLAN

SML Maschinengesellschaft mbH

Gewerbepark Ost 32, 4846 Redlham

ERDGESCHOSS

Maßstab 1:250



Stand: 7.09.2024

Plan Nr. **11** von **25**



TB JOSEF LEITNER
Hörzinghaider Strasse 3
A - 4623 Gunskirchen

Anschlussplan 09

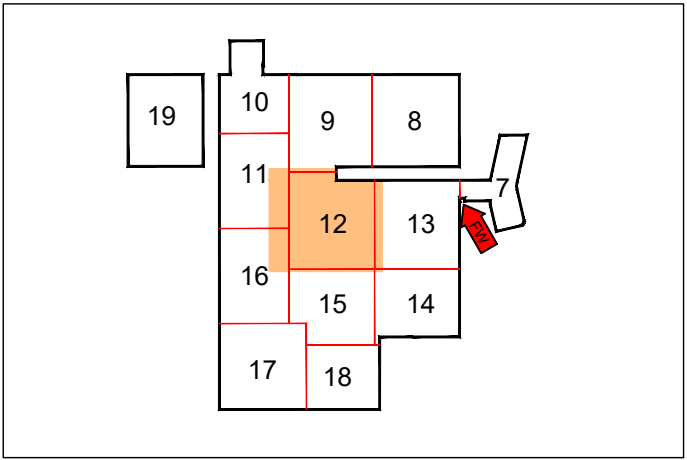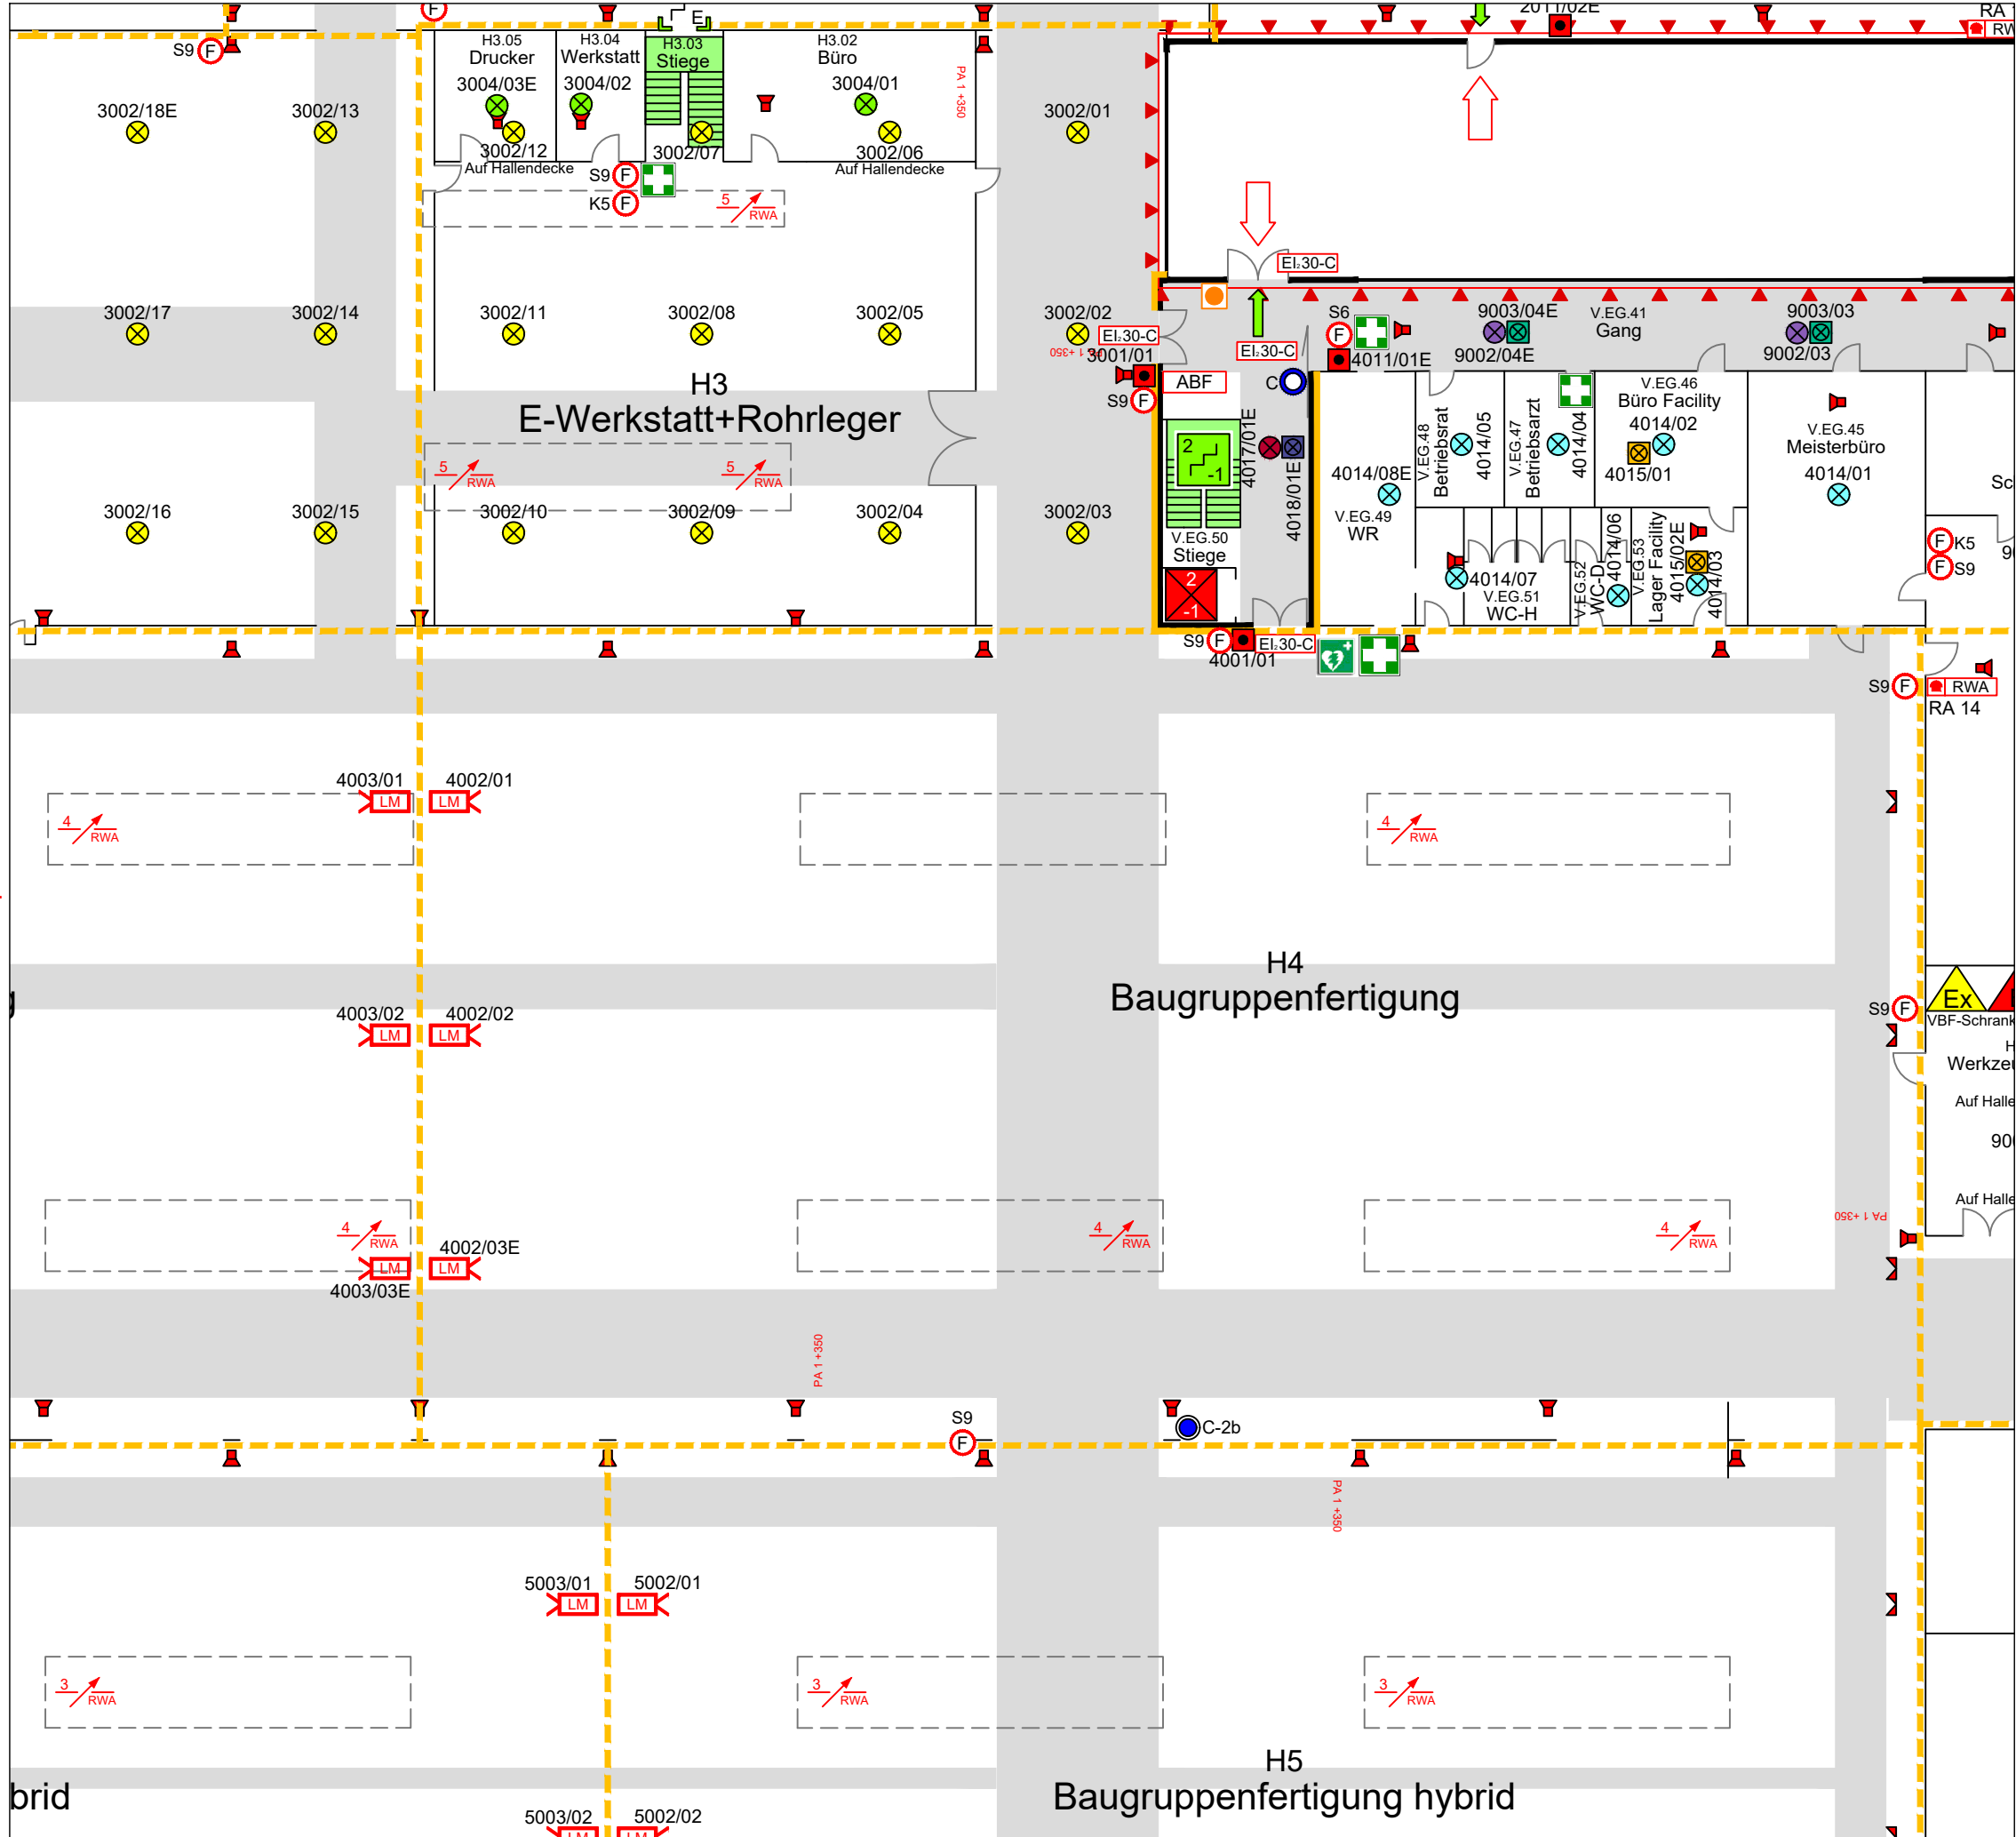

Übersichtsplan



2 / D
1
E / 00
K / -01

BRANDMELDEGRUPPEN:
DRUCKKNOPFMELDER:

3001 4001 4011

BRANDMELDER:

3002	3003	3004	4002	4003	4014
4015	4017	4018	5002	5003	9002
9003	9004	9005			




BRANDSCHUTZPLAN

SML Maschinengesellschaft mbH
Gewerbepark Ost 32, 4846 Redlham


ERDGESCHOSS

Maßstab 1:250 | Stand: 7.09.2024 | Plan Nr. **12** von **25**

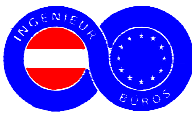

TB JOSEF LEITNER
Hörzinghaider Strasse 3
A - 4623 Gunskirchen

Anschlussplan 11

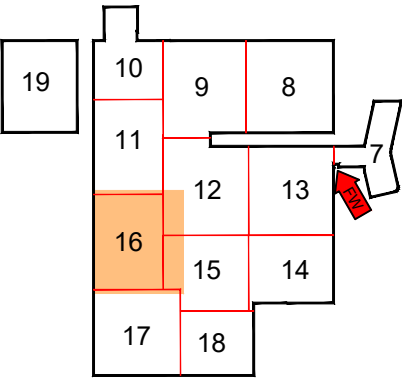

Übersichtsplan



E / 00
K / -01


Anschlussplan 15

BRANDMELDEGRUPPEN:
DRUCKKNOPFMELDER:

5001 6001

BRANDMELDER:

4002 4003 5002 5003 6002 6003

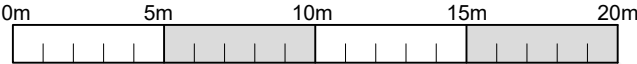

BRANDSCHUTZPLAN

SML Maschinengesellschaft mbH
Gewerbepark Ost 32, 4846 Redlham

ERDGESCHOSS


Maßstab 1:250 | Stand: 7.09.2024 | Plan Nr. 16 von 25




TB JOSEF LEITNER
Hörzinghaider Strasse 3
A - 4623 Gunskirchen

The floor plan illustrates a warehouse layout with the following details:



- Service Area (Top Left):** Includes rooms labeled H7.06 WC+DU extern, H7.03 Windfang, H7.02 Büro, H6.03 WC-H, H6.02 WC-D, H7.05 Lager, and H7.04 Cafe+Teek. It also shows various room numbers (e.g., 6001/04, 6004/01, 7004/01) and safety equipment like fire extinguishers (F) and fire alarm points (S9).
- H7 Versand (Middle):** A large open area labeled "H7 Versand".
- H8 Zwischenlager kalt (Bottom):** A large open area labeled "H8 Zwischenlager kalt".
- Structural Elements:** The plan shows a grid of columns and walls, with dashed lines indicating structural boundaries. A yellow dashed line runs horizontally across the middle of the plan.
- Safety and Technical Features:**
 - Fire Safety:** Multiple fire extinguishers (F) and fire alarm points (S9) are distributed throughout the facility. Red arrows labeled "RWA" (Rauchwarnanlage) indicate smoke alarm coverage.
 - Emergency Exits:** Red arrows labeled "z" indicate exit routes.
 - Specialized Equipment:** A "Löschanlage" (fire extinguishing system) and "Entstaubungsanlage" (dust removal system) are shown in the H8 area, along with a "Pulver" (powder) container.

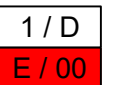

6002	6003	6004	7004
------	------	------	------

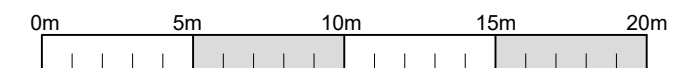Plan Nr. **17** von **25**

TB JOSEF LEITNER
Hörzinghaider Strasse 3
A - 4623 Gunskirchen

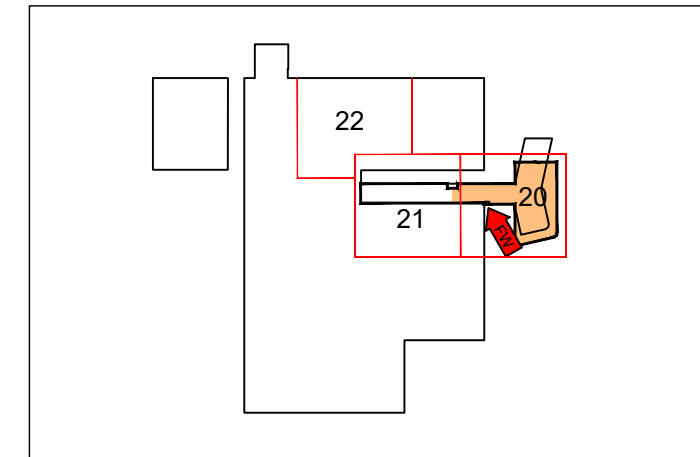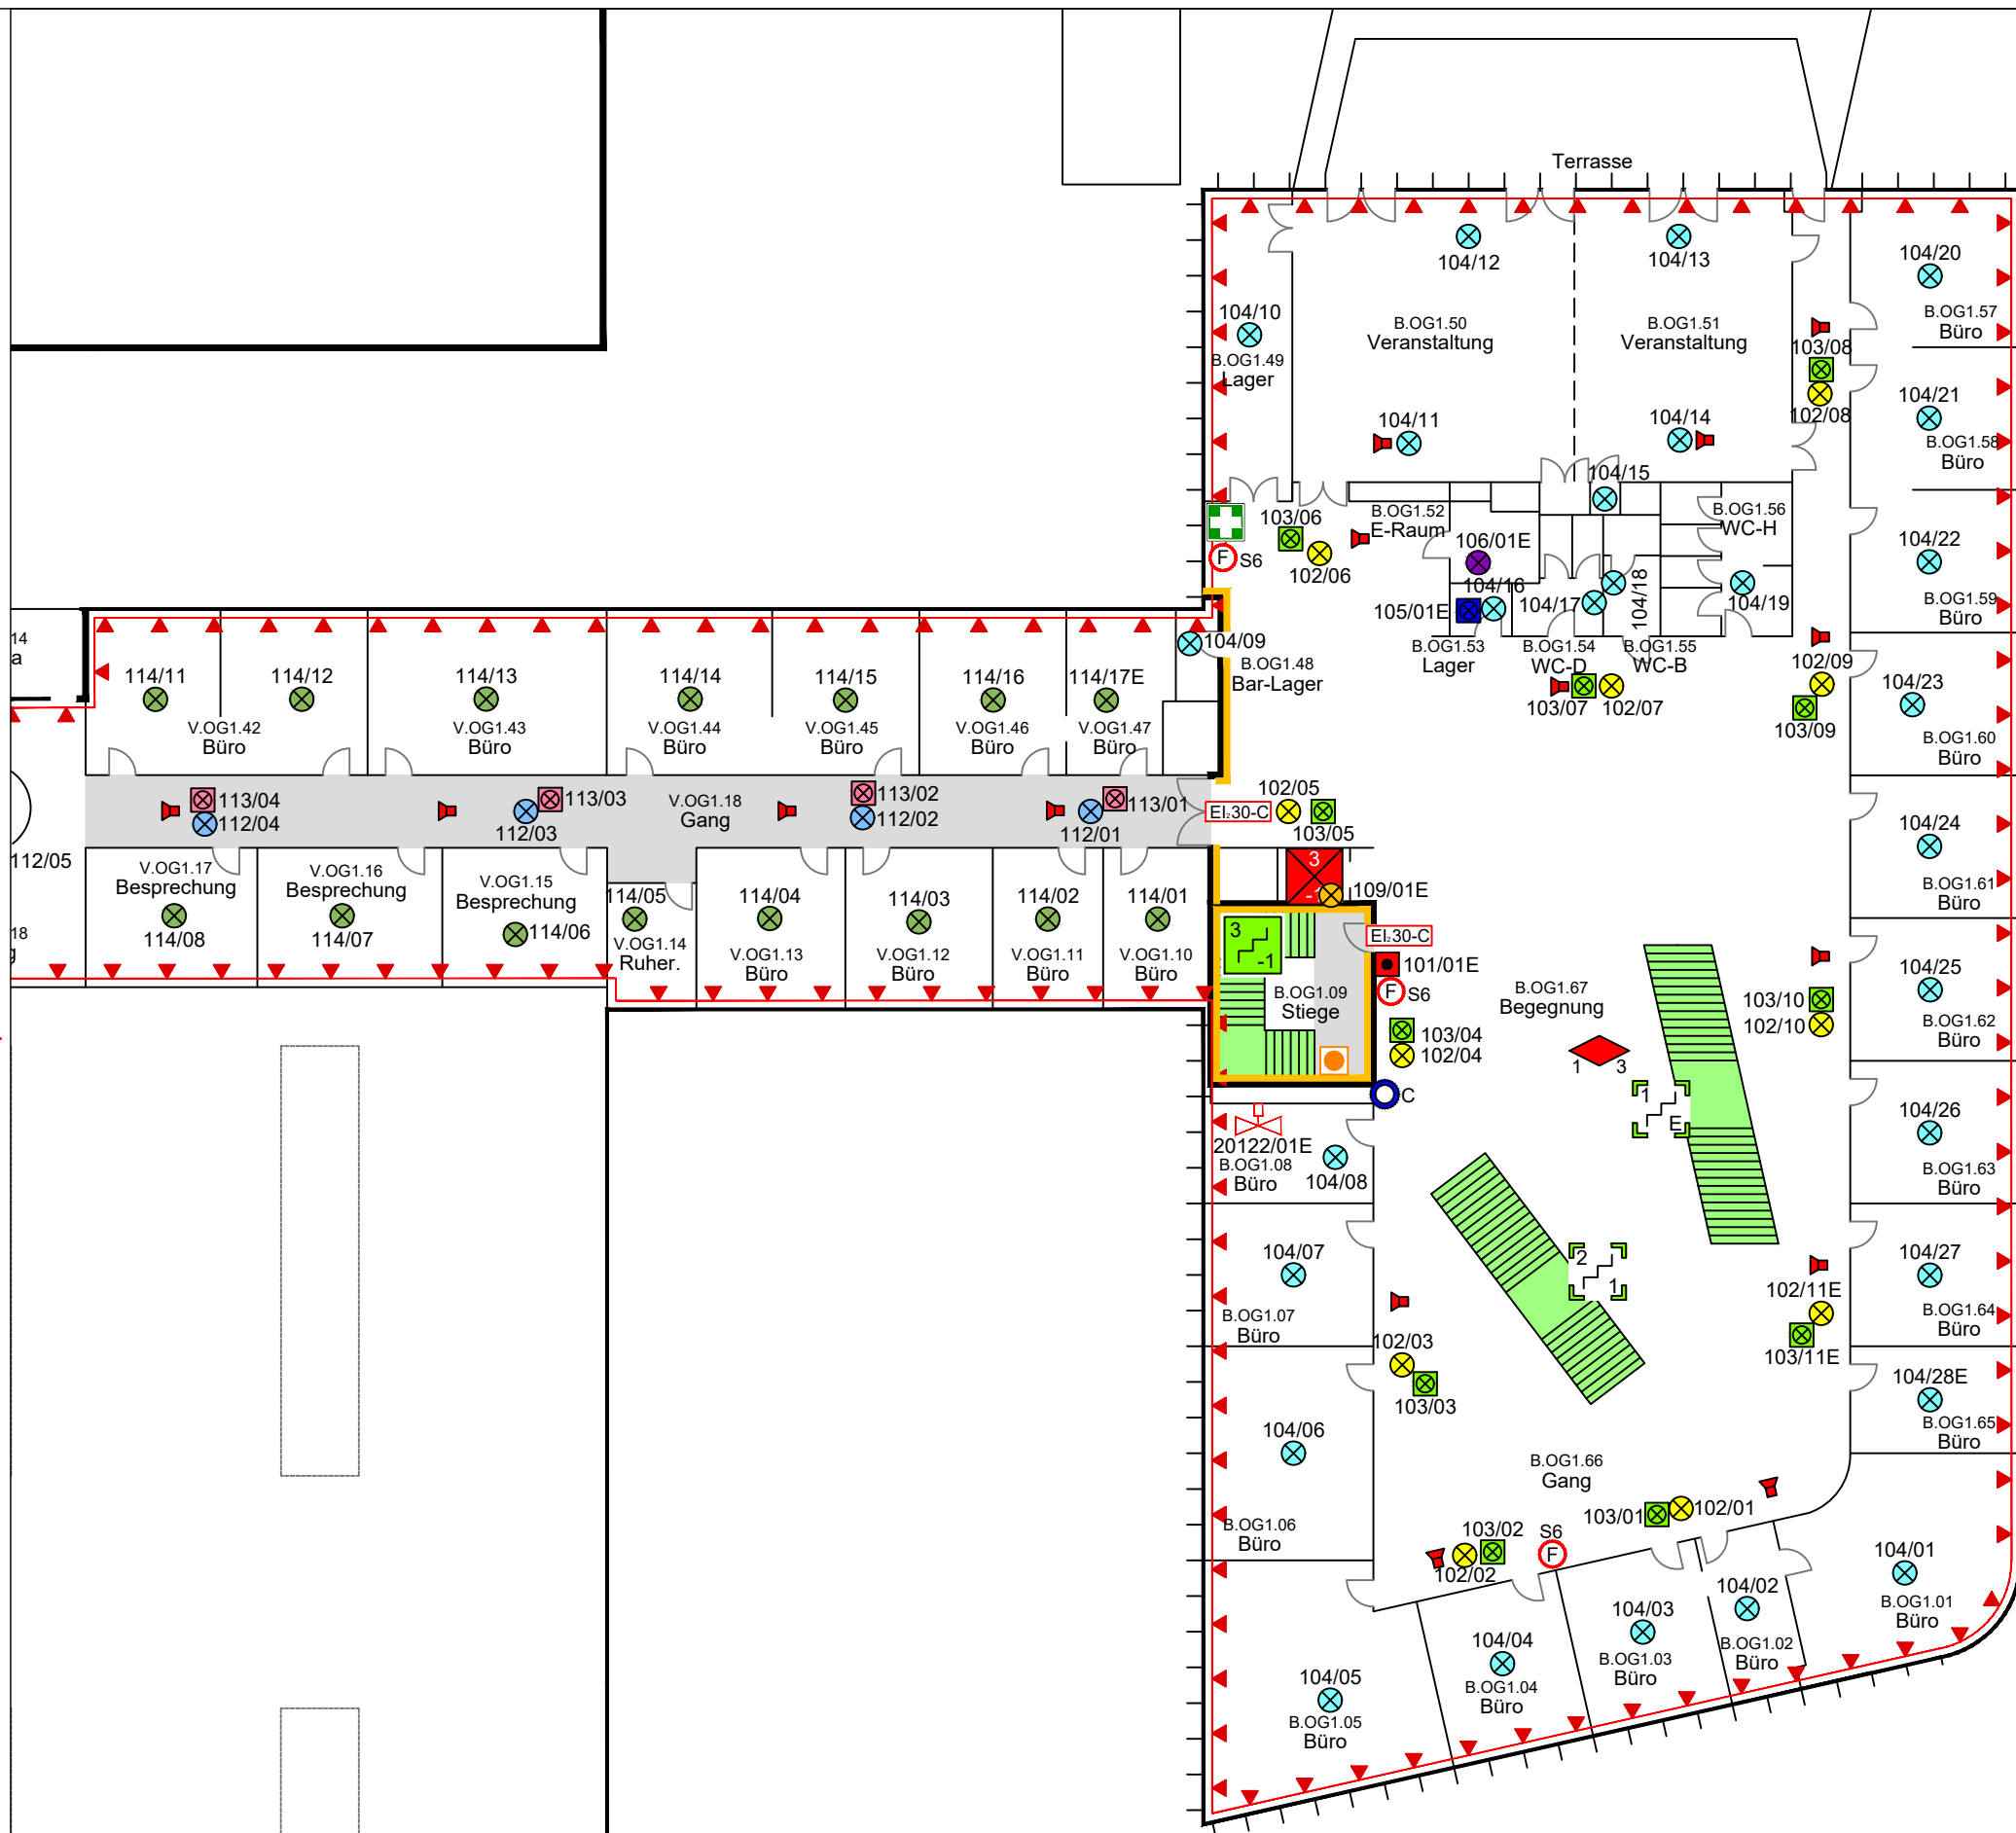

Übersichtsplan



3 / D
2
1
E / 00
K / -01

BRANDMELDEGRUPPEN:
DRUCKKNOPFMELDER:

101

BRANDMELDER:

102	103	104	105	106	109
112	113	114			

STRÖMUNGSWÄCHTER:

20122



BRANDSCHUTZPLAN

SML Maschinengesellschaft mbH

Gewerbepark Ost 32, 4846 Redlham

1.OBERGESCHOSS

Maßstab 1:250


Stand: 7.09.2024

Plan Nr. **20** von **25**



TB JOSEF LEITNER
Hörzinghaider Strasse 3
A - 4623 Gunskirchen

Anschlussplan 22

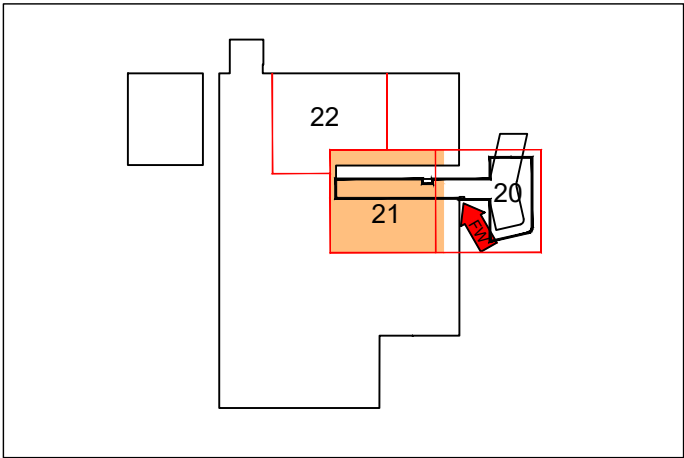

Übersichtsplan



2 / D
1
E / 00
K / -01

Anschlussplan 20

BRANDMELDEGRUPPEN:
DRUCKKNOPFMELDER:

111 121

BRANDMELDER:

112	113	114	118	122	123
124	126	128	129		




BRANDSCHUTZPLAN



SML Maschinengesellschaft mbH
Gewerbepark Ost 32, 4846 Redlham

1.OBERGESCHOSS

Maßstab 1:250 Stand: 7.09.2024 Plan Nr. 21 von 25

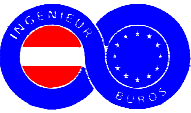

TB JOSEF LEITNER
Hörzinghaider Strasse 3
A - 4623 Gunskirchen

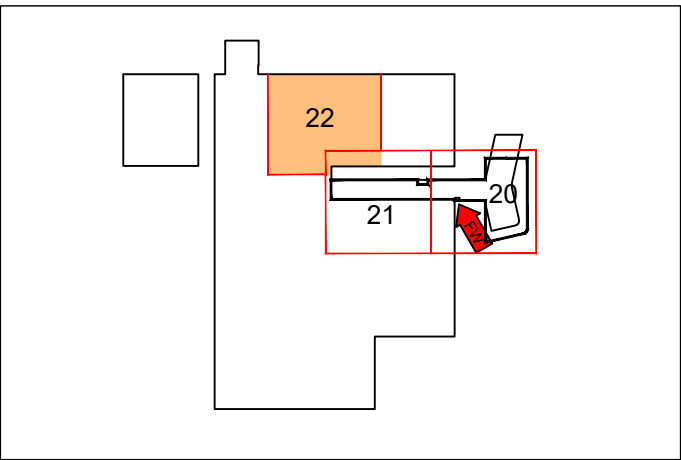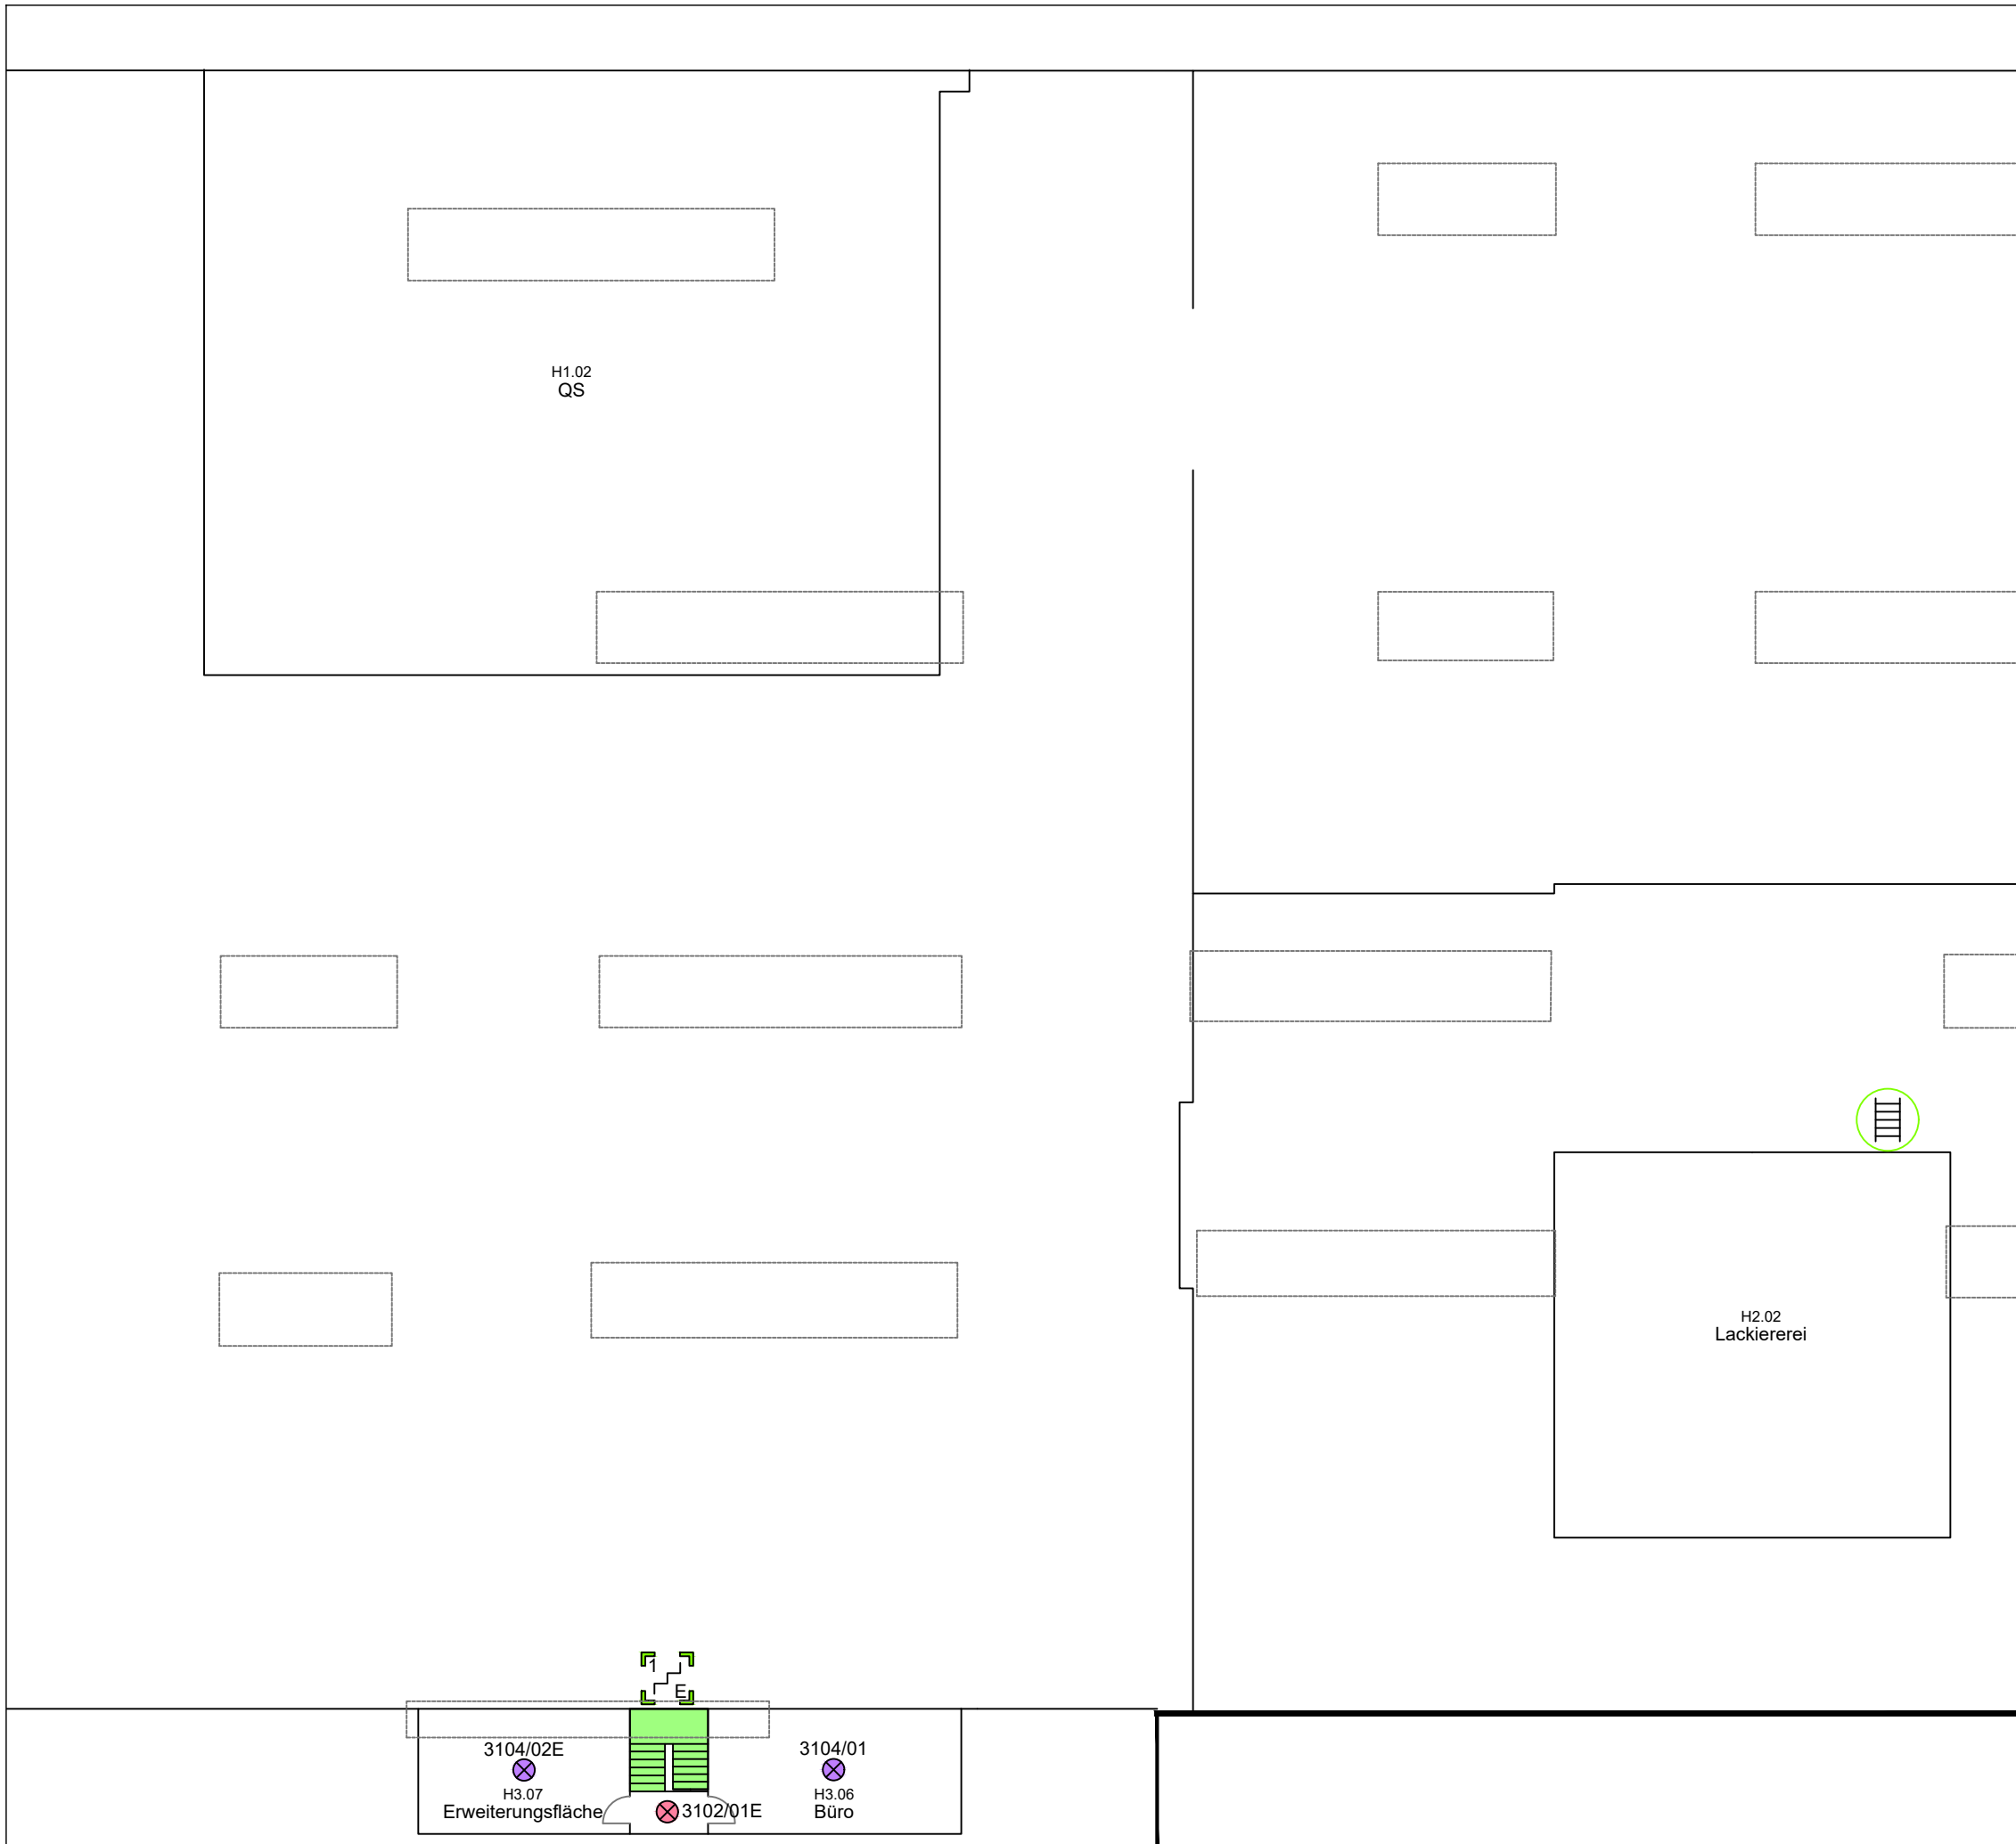

Übersichtsplan



1 / D
E / 00
K / -01

BRANDMELDEGRUPPEN:
DRUCKKNOPFMELDER:

BRANDMELDER:

3102	3104
------	------




BRANDSCHUTZPLAN



SML Maschinengesellschaft mbH
Gewerbepark Ost 32, 4846 Redlham

1.OBERGESCHOSS

Maßstab 1:250 | Stand: 7.09.2024 | Plan Nr. **22** von **25**

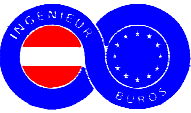

TB JOSEF LEITNER
Hörzinghaider Strasse 3
A - 4623 Gunskirchen

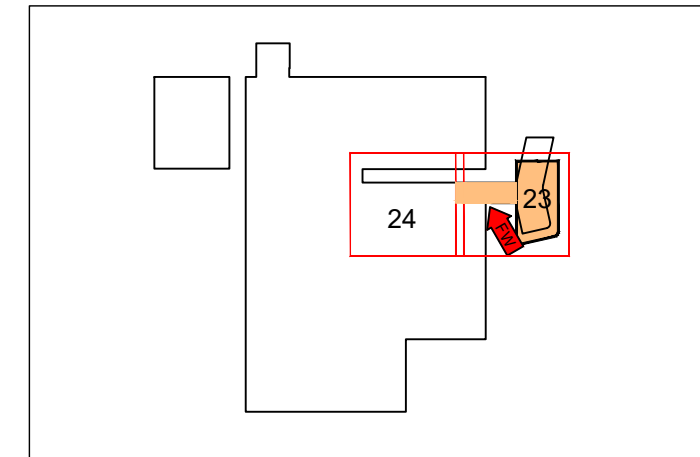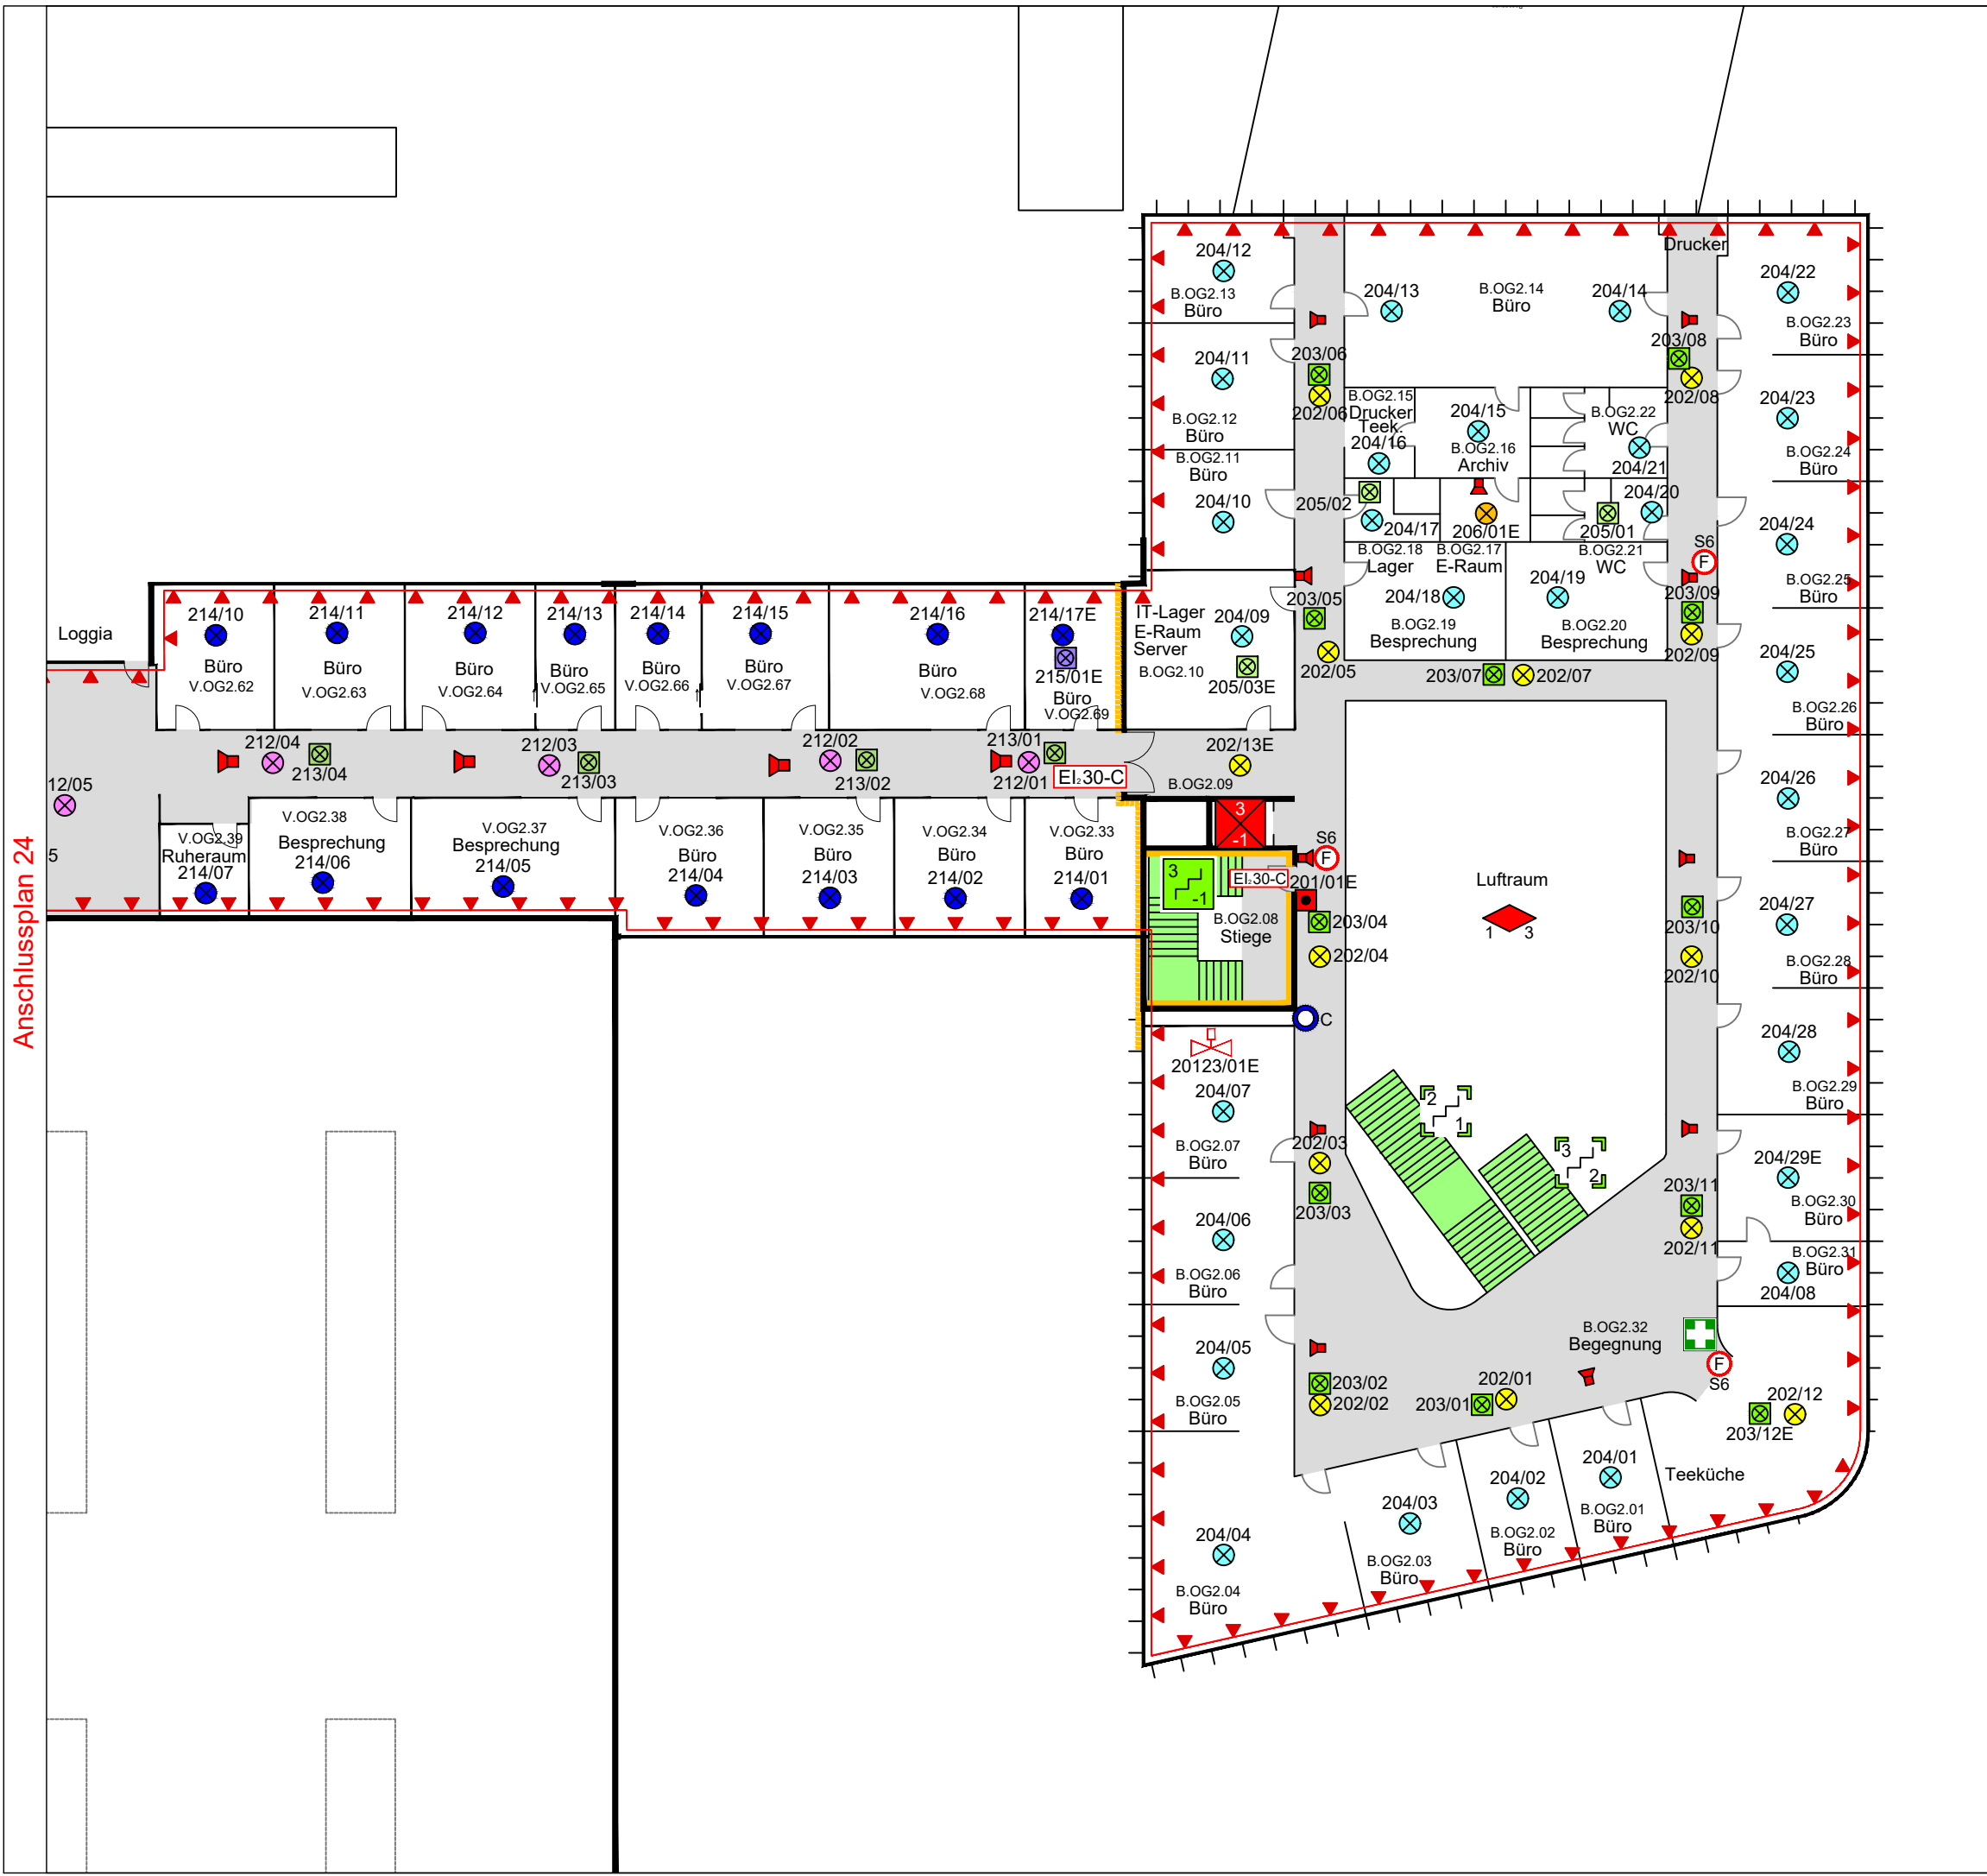

Übersichtsplan



3 / D
2
1
E / 00
K / -01

BRANDMELDEGRUPPEN:
DRUCKKNOPFMELDER:

201

BRANDMELDER:

202	203	204	205	206
212	213	214	215	

STRÖMUNGSWÄCHTER:

20123



BRANDSCHUTZPLAN

SML Maschinengesellschaft mbH


Gewerbepark Ost 32, 4846 Redlham

2.OBERGESCHOSS



Maßstab 1:250

Stand: 7.09.2024

Plan Nr. **23** von **25**

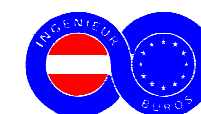

TB JOSEF LEITNER
Hörzinghaider Strasse 3
A - 4623 Gunskirchen

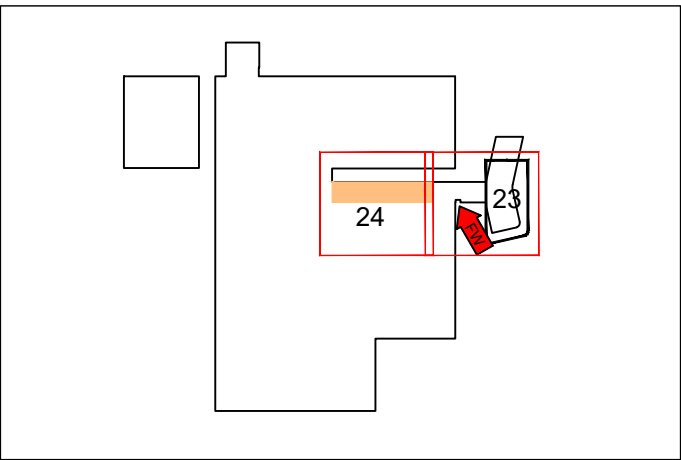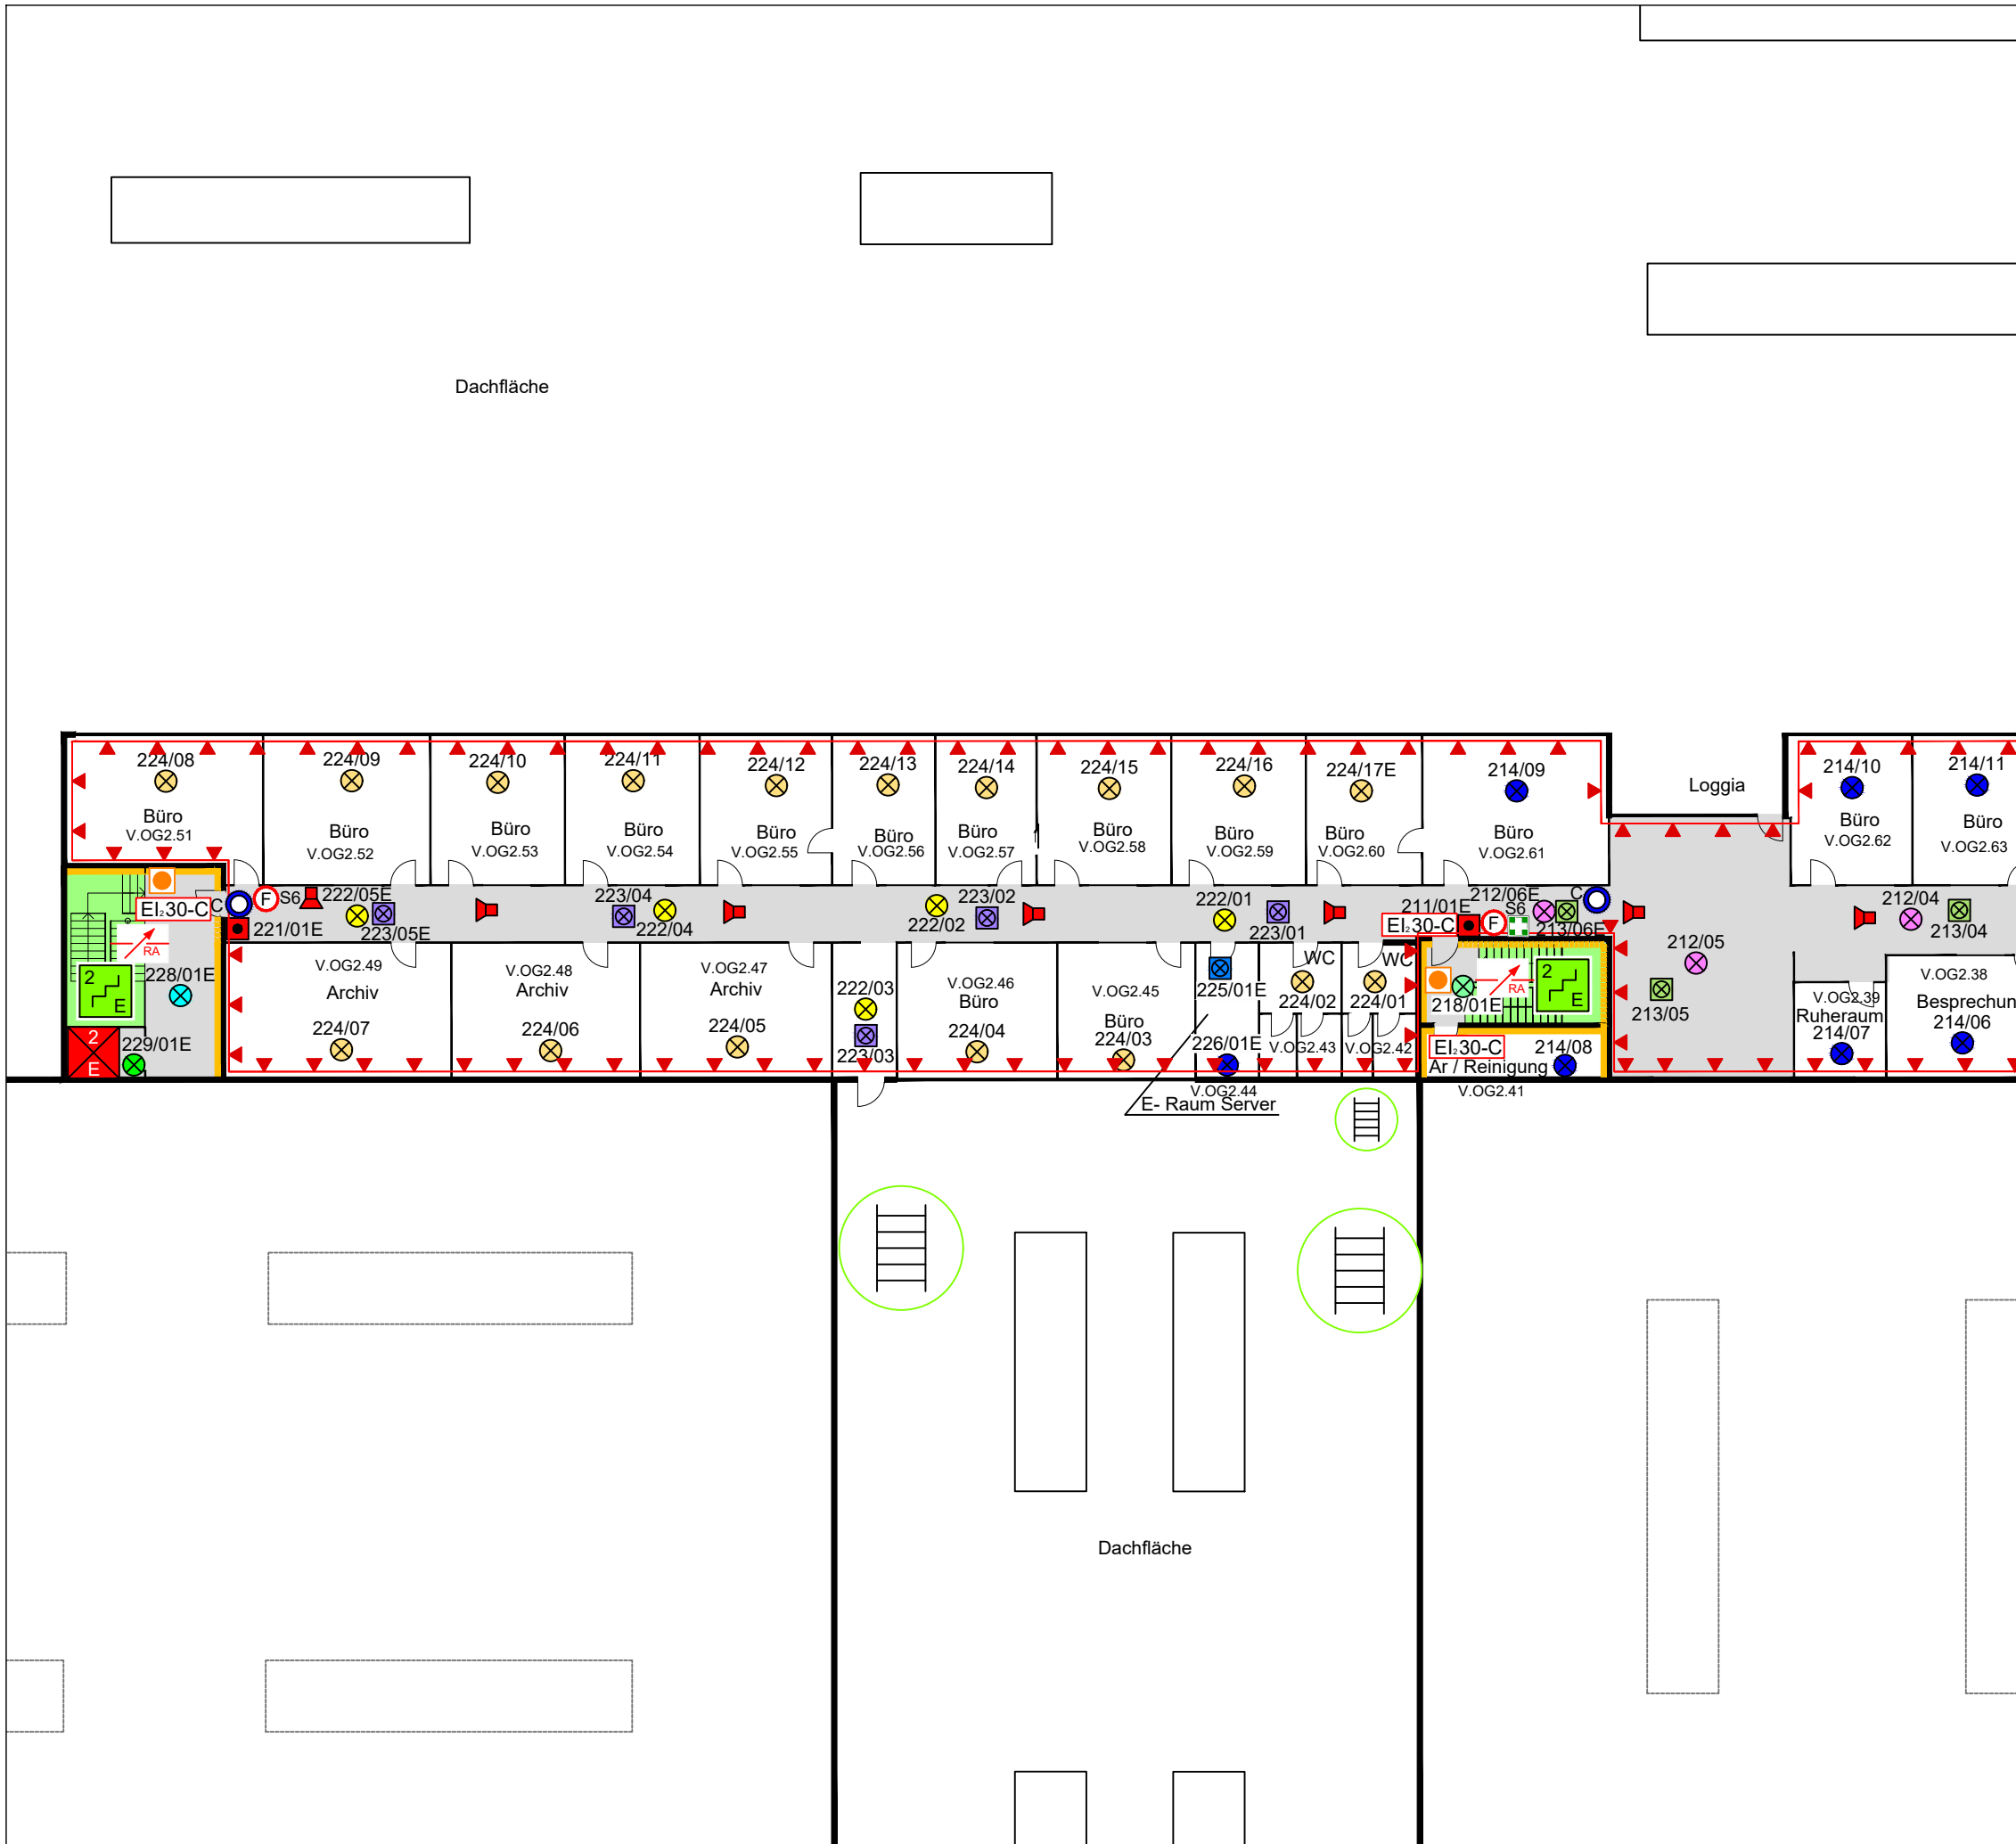

Übersichtsplan



2 / D
1
E / 00
K / -01

Anschlussplan 23

BRANDMELDEGRUPPEN:
DRUCKKNOPFMELDER:

211 221

BRANDMELDER:

212	213	214	218	222	223
224	225	228	229		




BRANDSCHUTZPLAN



SML Maschinengesellschaft mbH
Gewerbepark Ost 32, 4846 Redlham

2.OBERGESCHOSS

Maßstab 1:250 Stand: 7.09.2024 Plan Nr. **24** von **25**

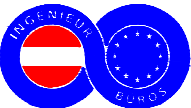

TB JOSEF LEITNER
Hörzinghaider Strasse 3
A - 4623 Gunskirchen

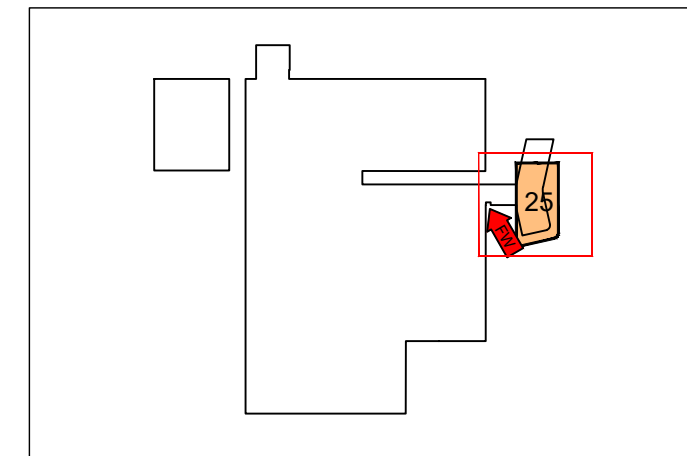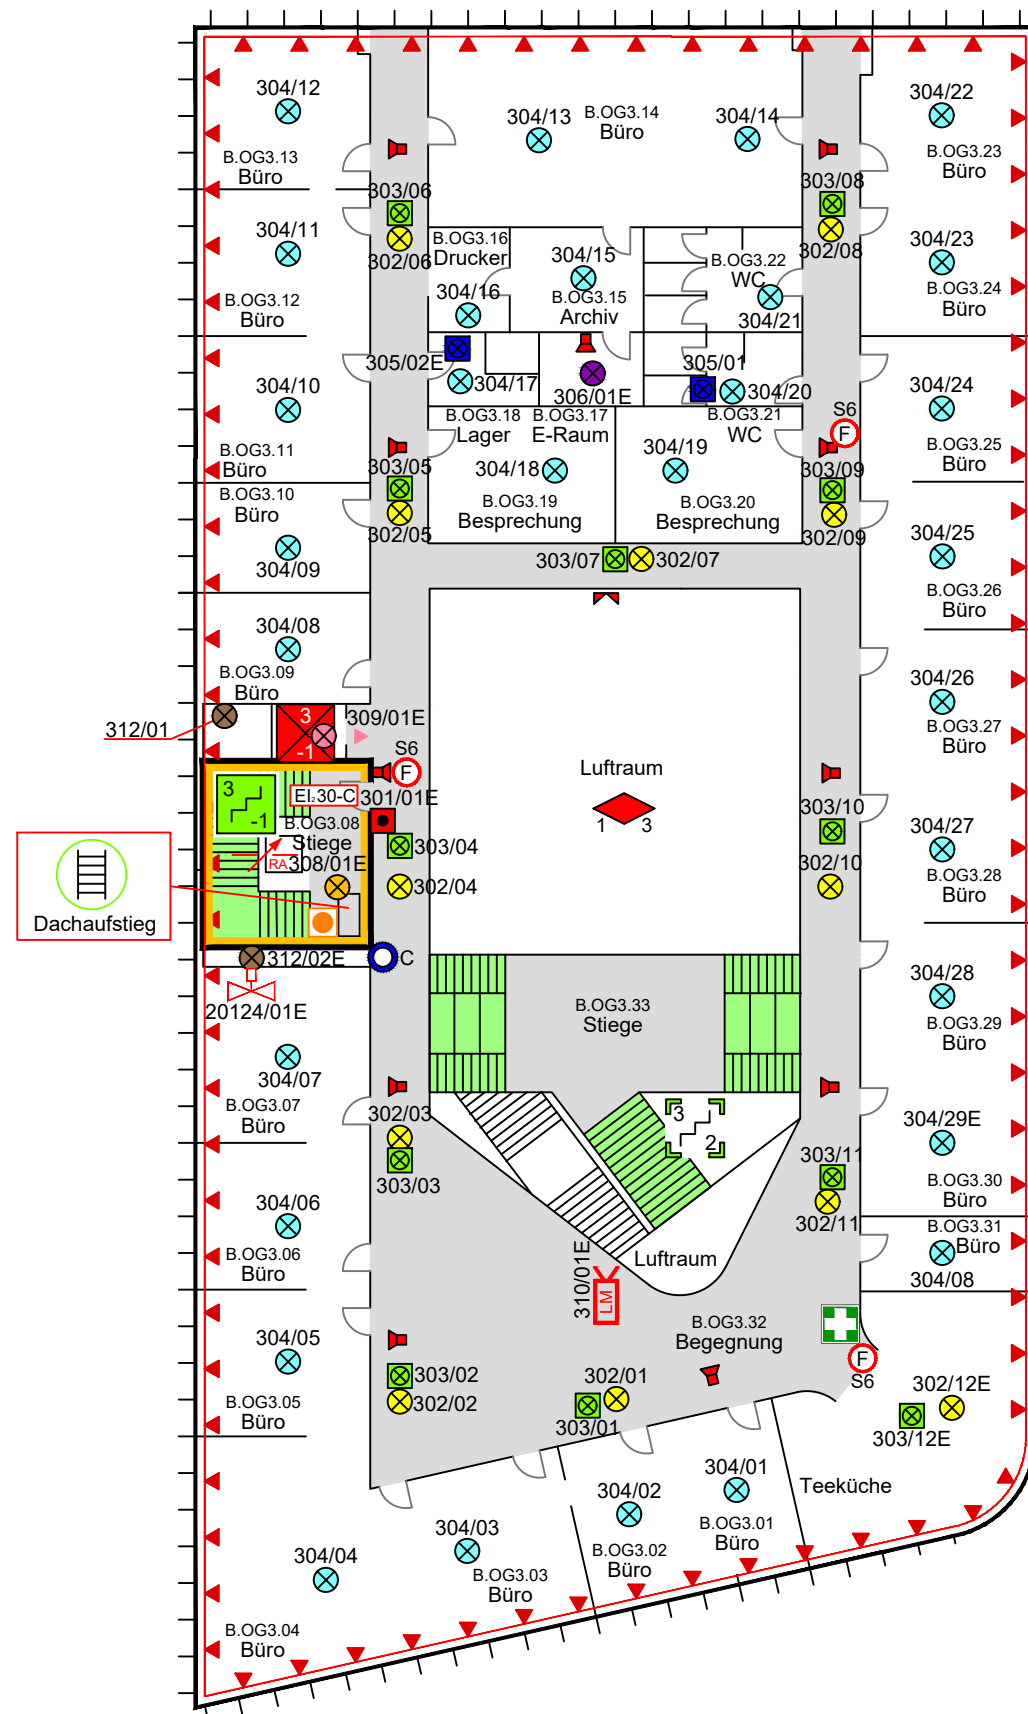

Übersichtsplan



3 / D
2
1
E / 00
K / -01

BRANDMELDEGRUPPEN:
DRUCKKNOPFMELDER:


301

BRANDMELDER:

302	303	304	305	306	308
309	310	312			

STRÖMUNGSWÄCHTER:

20124

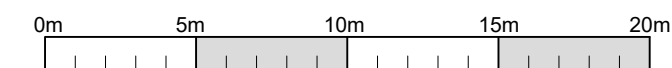

BRANDSCHUTZPLAN

SML Maschinengesellschaft mbH

Gewerbepark Ost 32, 4846 Redlham

3.OBERGESCHOSS

Maßstab 1:250

Stand: 7.09.2024

Plan Nr. **25** von **25**



TB JOSEF LEITNER
Hörzinghaider Strasse 3
A - 4623 Gunskirchen